

PERENCANAAN DED PRIMAUSADA SUKOREJO
Gambar Detail Engineering Design (DED)


—BANGUNAN UGD PRIMAUSADA SUKOREJO—

Gambar Detail Struktur

DAFTAR ISI


NO	NO. GAMBAR	JUDUL GAMBAR	SKALA
0	STRUKTUR		
1	—	DAFTAR GAMBAR 1	NTS
2	S.1.01	DENAH PONDASI	1 : 200 PAPER A3
3	S.2.01	DENAH KOLOM	1 : 200 PAPER A3
4	S.3.01	DENAH SLOOF	1 : 200 PAPER A3
5	S.4.01	DENAH KOLOM BAJA	1 : 200 PAPER A3
6	S.5.01	DENAH BALOK BAJA +4.00	1 : 200 PAPER A3
7	S.5.02	DENAH BALOK BAJA +7.85	1 : 200 PAPER A3
8	S.5.03	DENAH BALOK BAJA +11.70	1 : 200 PAPER A3
9	S.5.04	DENAH BALOK BAJA +15.55	1 : 200 PAPER A3
10	S.5.05	DENAH BALOK BAJA +19.40	1 : 200 PAPER A3
11	S.6.01	DENAH PLAT LANTAI +4.15	1 : 200 PAPER A3
12	S.6.02	DENAH PLAT LANTAI +8.00	1 : 200 PAPER A3
13	S.6.03	DENAH PLAT LANTAI +11.85	1 : 200 PAPER A3
14	S.6.04	DENAH PLAT LANTAI +15.70	1 : 200 PAPER A3
15	S.6.05	DENAH PLAT LANTAI +19.55	1 : 200 PAPER A3
16	S.7.01	DETAIL STRUKTUR	1 : 25 PAPER A3
17	S.7.02	DETAIL STRUKTUR	1 : 25 PAPER A3
18	S.7.03	DETAIL STRUKTUR	1 : 25 PAPER A3
19	S.7.04	DETAIL STRUKTUR	1 : 15 PAPER A3
20	S.7.05	DETAIL STRUKTUR	1 : 15 PAPER A3


KETERANGAN			
REVISI			
NO.	URAIAN	TANGGAL	PARAF
PEMBERI TUGAS :			
NAMA PROYEK :			
PERENCANAAN DED PRIMAHUSADA SUKOREJO			
MENGETAHUI:			
PEMILIK			
KONSULTAN PERENCANA :			
 PT.ASKA MULIA ANOPAMA <i>architecture.interior.and urban design</i> Jl.Prambanan-Piyungan KM.1,5 no.8 Ngoro-Oro, Ringinsari, Bokoharjo, Prambanan, Sleman, Yogyakarta, 55572			
PENANGGUNG JAWAB ARSITEKTUR:			
 AGUS SETIAWAN,ST.,M.Arch.,IAI,GP AHLI ARSITEK—MADYA			
PENANGGUNG JAWAB STRUKTUR:			
 WAHYU HENDRATNO, ST AHLI TEKNIK BANGUNAN GEDUNG—MADYA			
PENANGGUNG JAWAB MEKANIKAL—ELEKTRIKAL—PLUMBING:			
 NOVA NURDIANSYAH, ST AHLI TEKNIK TENAGA LISTRIK—MADYA			
NAMA GAMBAR :			
DAFTAR ISI			
NO. PROYEK :		TANGGAL :	
—		DIGAMBAR :	
SATUAN UKURAN :		DIPERIKSA :	
		DISETUJUI :	
SKALA	NO. GAMBAR	NO. REVISI	NO. LEMBAR
NTS	S		0

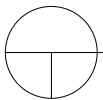


DENAH PONDASI

SKALA 1: 200 PAPER A3

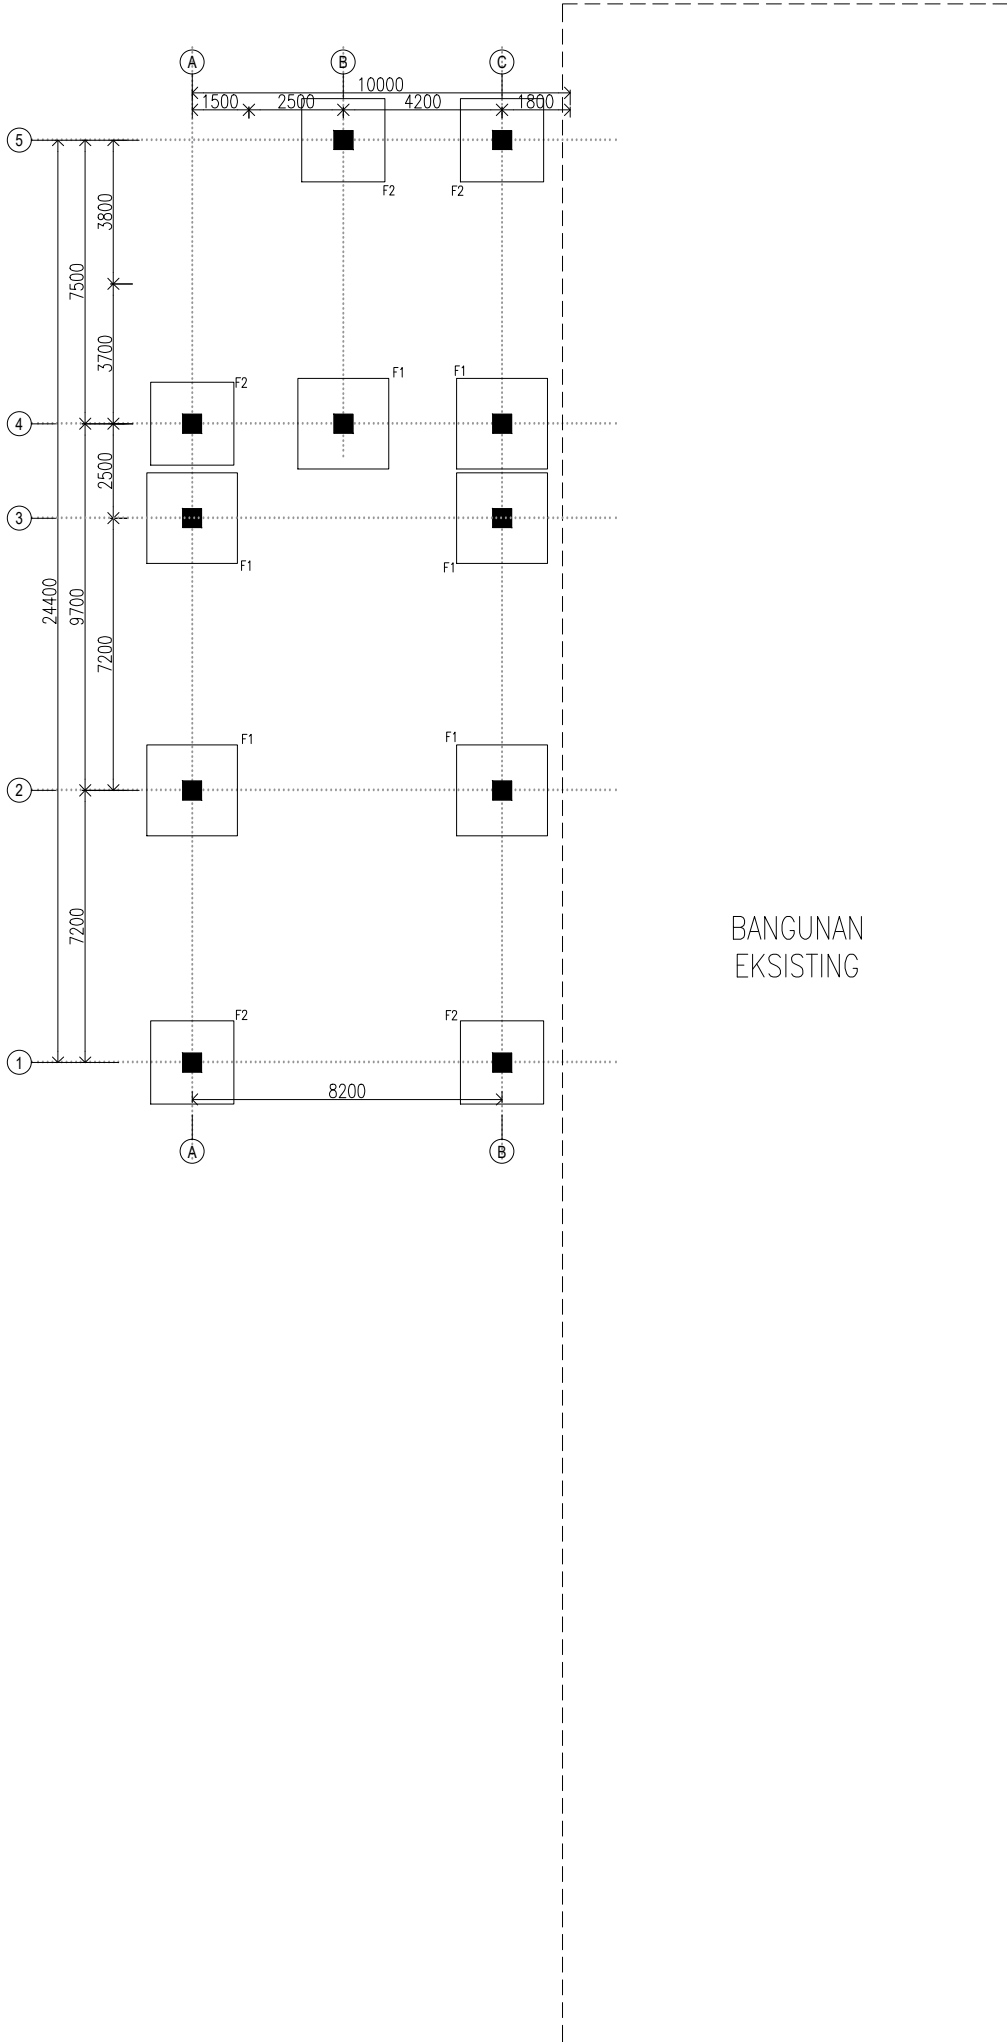

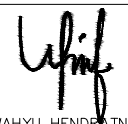KETERANGAN			
REVISI			
NO.	URAIAN	TANGGAL	PARAF
PEMBERI TUGAS :			
NAMA PROYEK :			
PERENCANAAN DED PRIMAHUSADA SUKOREJO			
MENGETAHUI:			
PEMILIK			
KONSULTAN PERENCANA :			
 PT.ASKA MULIA ANOPAMA <i>architecture.interior.and urban design</i> Jl.Prambanan-Piyungan KM.1,5 no.8 Ngoro-Oro, Ringinsari, Bokoharjo, Prambanan, Sleman, Yogyakarta, 55572			
PENANGGUNG JAWAB ARSITEKTUR:			
 AGUS SETIAWAN,ST.,M.Arch.,IAI,GP AHLI ARSITEK—MADYA			
PENANGGUNG JAWAB STRUKTUR:			
 WAHYU HENDRATNO, ST AHLI TEKNIK BANGUNAN GEDUNG—MADYA			
PENANGGUNG JAWAB MEKANIKAL—ELEKTRIKAL—PLUMBING:			
 NOVA NURDIANSYAH, ST AHLI TEKNIK TENAGA LISTRIK—MADYA			
NAMA GAMBAR :			
DENAH PONDASI			
NO. PROYEK :		TANGGAL :	
—		DIGAMBAR :	
SATUAN UKURAN :		DIPERIKSA :	
		DISETUJUI :	
SKALA	NO. GAMBAR	NO. REVISI	NO. LEMBAR
1:200 PAPER A3	S.1.01		1

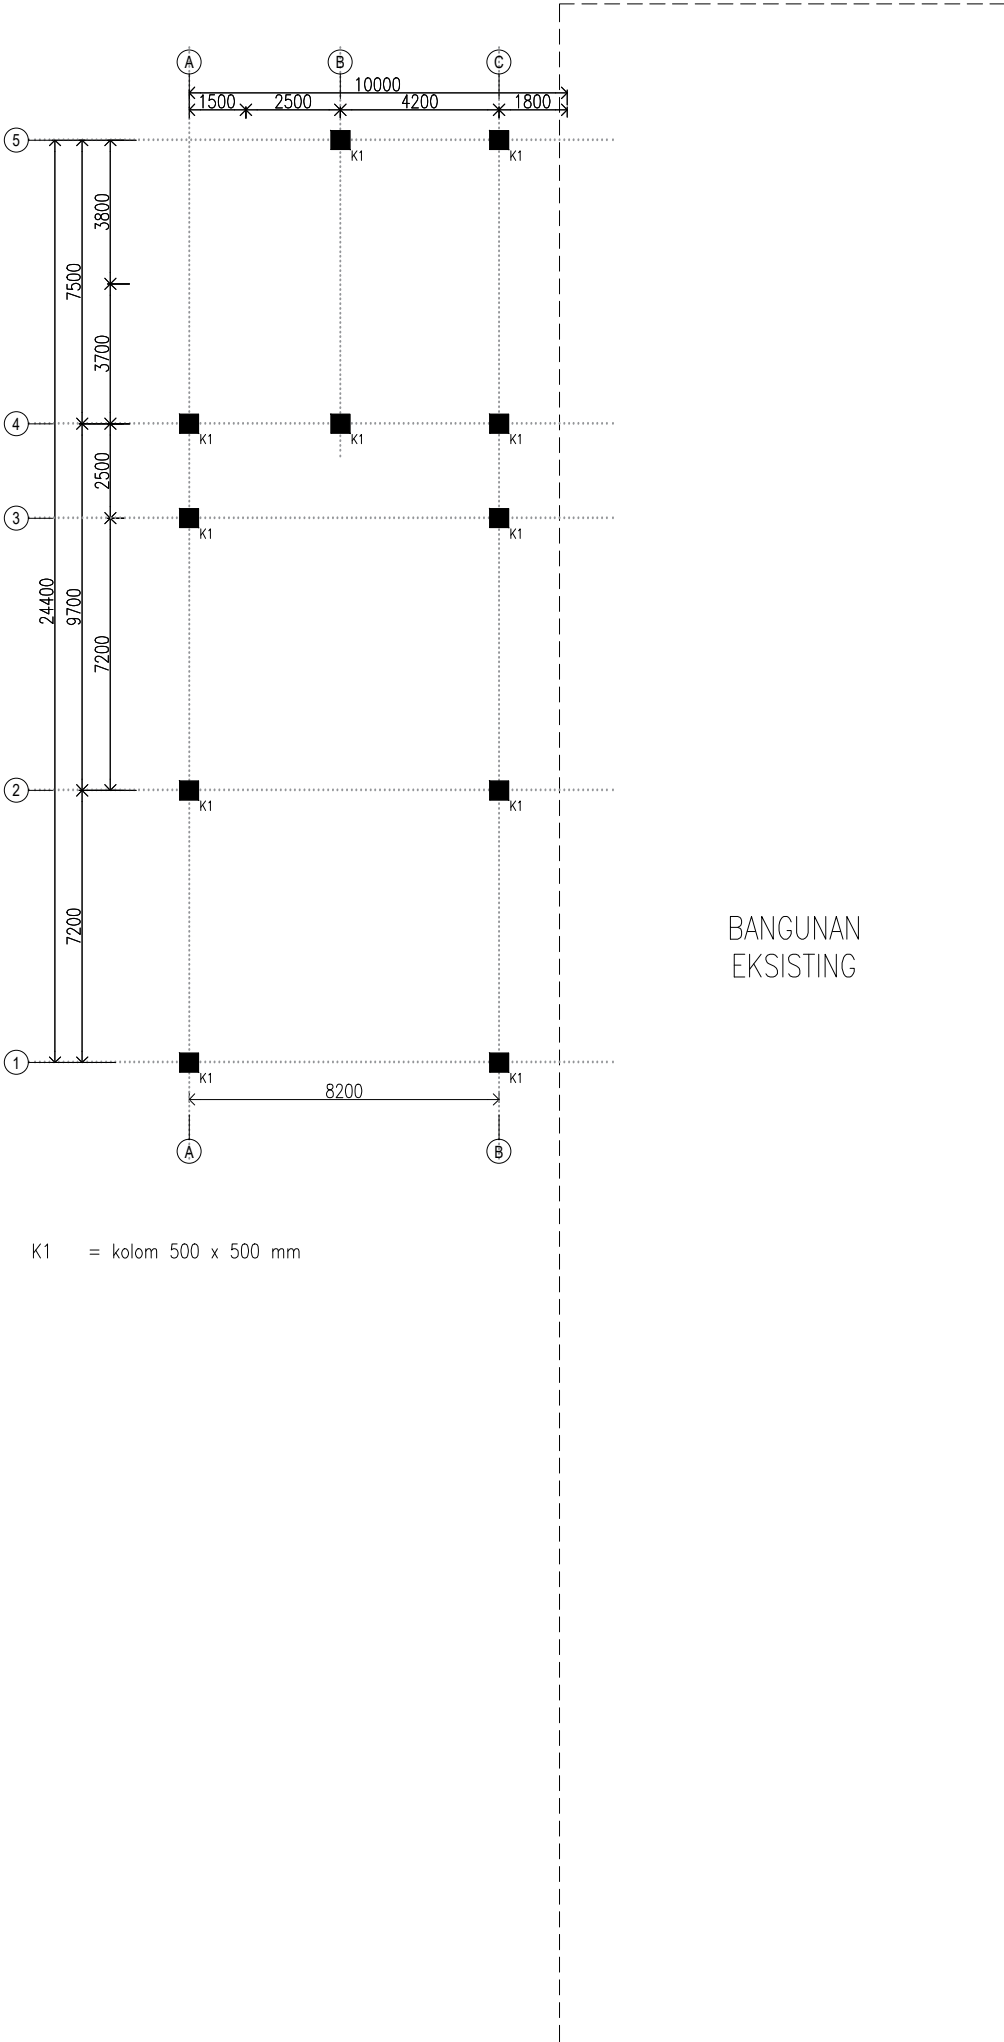


KETERANGAN			
REVISI			
NO.	URAIAN	TANGGAL	PARAF
PEMBERI TUGAS :			
NAMA PROYEK :			
PERENCANAAN DED PRIMAUSADA SUKOREJO			
MENGETAHUI:			
PEMILIK			
KONSULTAN PERENCANA :			
PT.ASKA MULIA ANOPAMA architecture.interior.and urban design Jl.Prambanan-Piyungan KM.1,5 no.8 Ngoro-Oro, Ringinsari, Bokoharjo, Prambanan, Sleman, Yogyakarta, 55572			
PENANGGUNG JAWAB ARSITEKTUR:			
AGUS SETIAWAN,ST.,M.Arch.,IAI,GP AHLI ARSITEK—MADYA			
PENANGGUNG JAWAB STRUKTUR:			
WAHYU HENDRATNO, ST AHLI TEKNIK BANGUNAN GEDUNG—MADYA			
PENANGGUNG JAWAB MEKANIKAL—ELEKTRIKAL—PLUMBING:			
NOVA NURDIANSYAH, ST AHLI TEKNIK TENAGA LISTRIK—MADYA			
NAMA GAMBAR :			
DENAH KOLOM			
NO. PROYEK :		TANGGAL :	
—		DIGAMBAR :	
SATUAN UKURAN :		DIPERIKSA :	
		DISETUJUI :	
SKALA	NO. GAMBAR	NO. REVISI	NO. LEMBAR
1:200 PAPER A3	S.2.01		2



DENAH SLOOF


SKALA 1: 200 PAPER A3

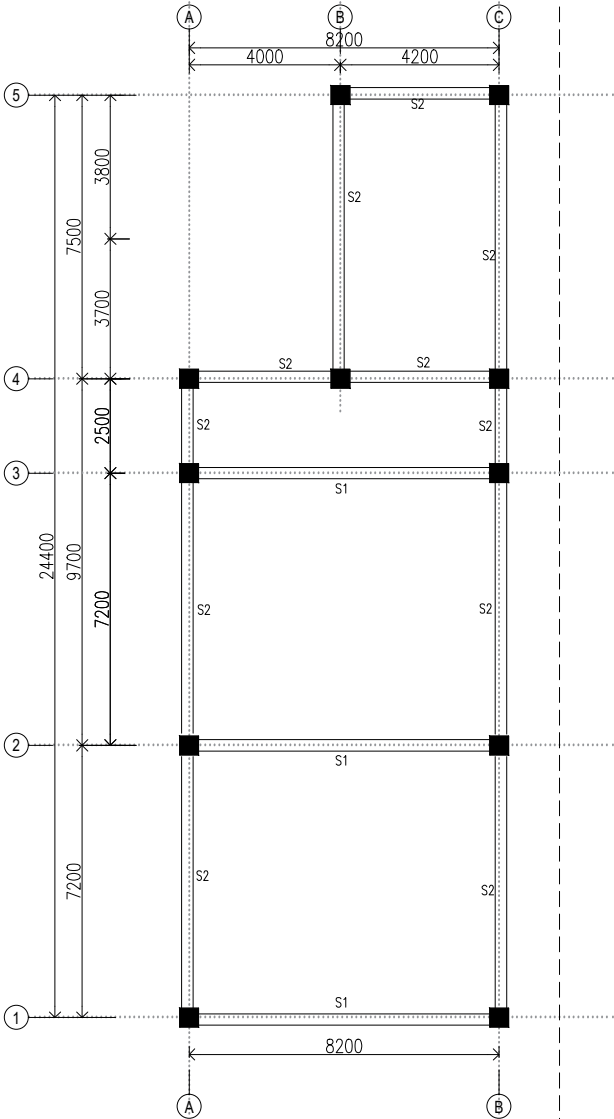


S1 = sloof 300 x 600 mm
S2 = sloof 300 x 500 mm

BANGUNAN
EKSISTING

KETERANGAN			
REVISI			
NO.	URAIAN	TANGGAL	PARAF
PEMBERI TUGAS :			
NAMA PROYEK :			
PERENCANAAN DED PRIMAHUSADA SUKOREJO			
MENGETAHUI:			
PEMILIK			
KONSULTAN PERENCANA :			
 PT.ASKA MULIA ANOPAMA <i>architecture.interior.and urban design</i> Jl.Prambanan-Piyungan KM.1,5 no.8 Ngoro-Oro, Ringinsari, Bokoharjo, Prambanan, Sleman, Yogyakarta, 55572			
PENANGGUNG JAWAB ARSITEKTUR:			
 AGUS SETIAWAN,ST.,M.Arch.,IAI,GP AHLI ARSITEK—MADYA			
PENANGGUNG JAWAB STRUKTUR:			
 WAHYU HENDRATNO, ST AHLI TEKNIK BANGUNAN GEDUNG—MADYA			
PENANGGUNG JAWAB MEKANIKAL—ELEKTRIKAL—PLUMBING:			
 NOVA NURDIANSYAH, ST AHLI TEKNIK TENAGA LISTRIK—MADYA			
NAMA GAMBAR :			
DENAH SLOOF			
NO. PROYEK :		TANGGAL :	
—		DIGAMBAR :	
SATUAN UKURAN :		DIPERIKSA :	
		DISETUJUI :	
SKALA	NO. GAMBAR	NO. REVISI	NO. LEMBAR
1:200 PAPER A3	S.3.01		3

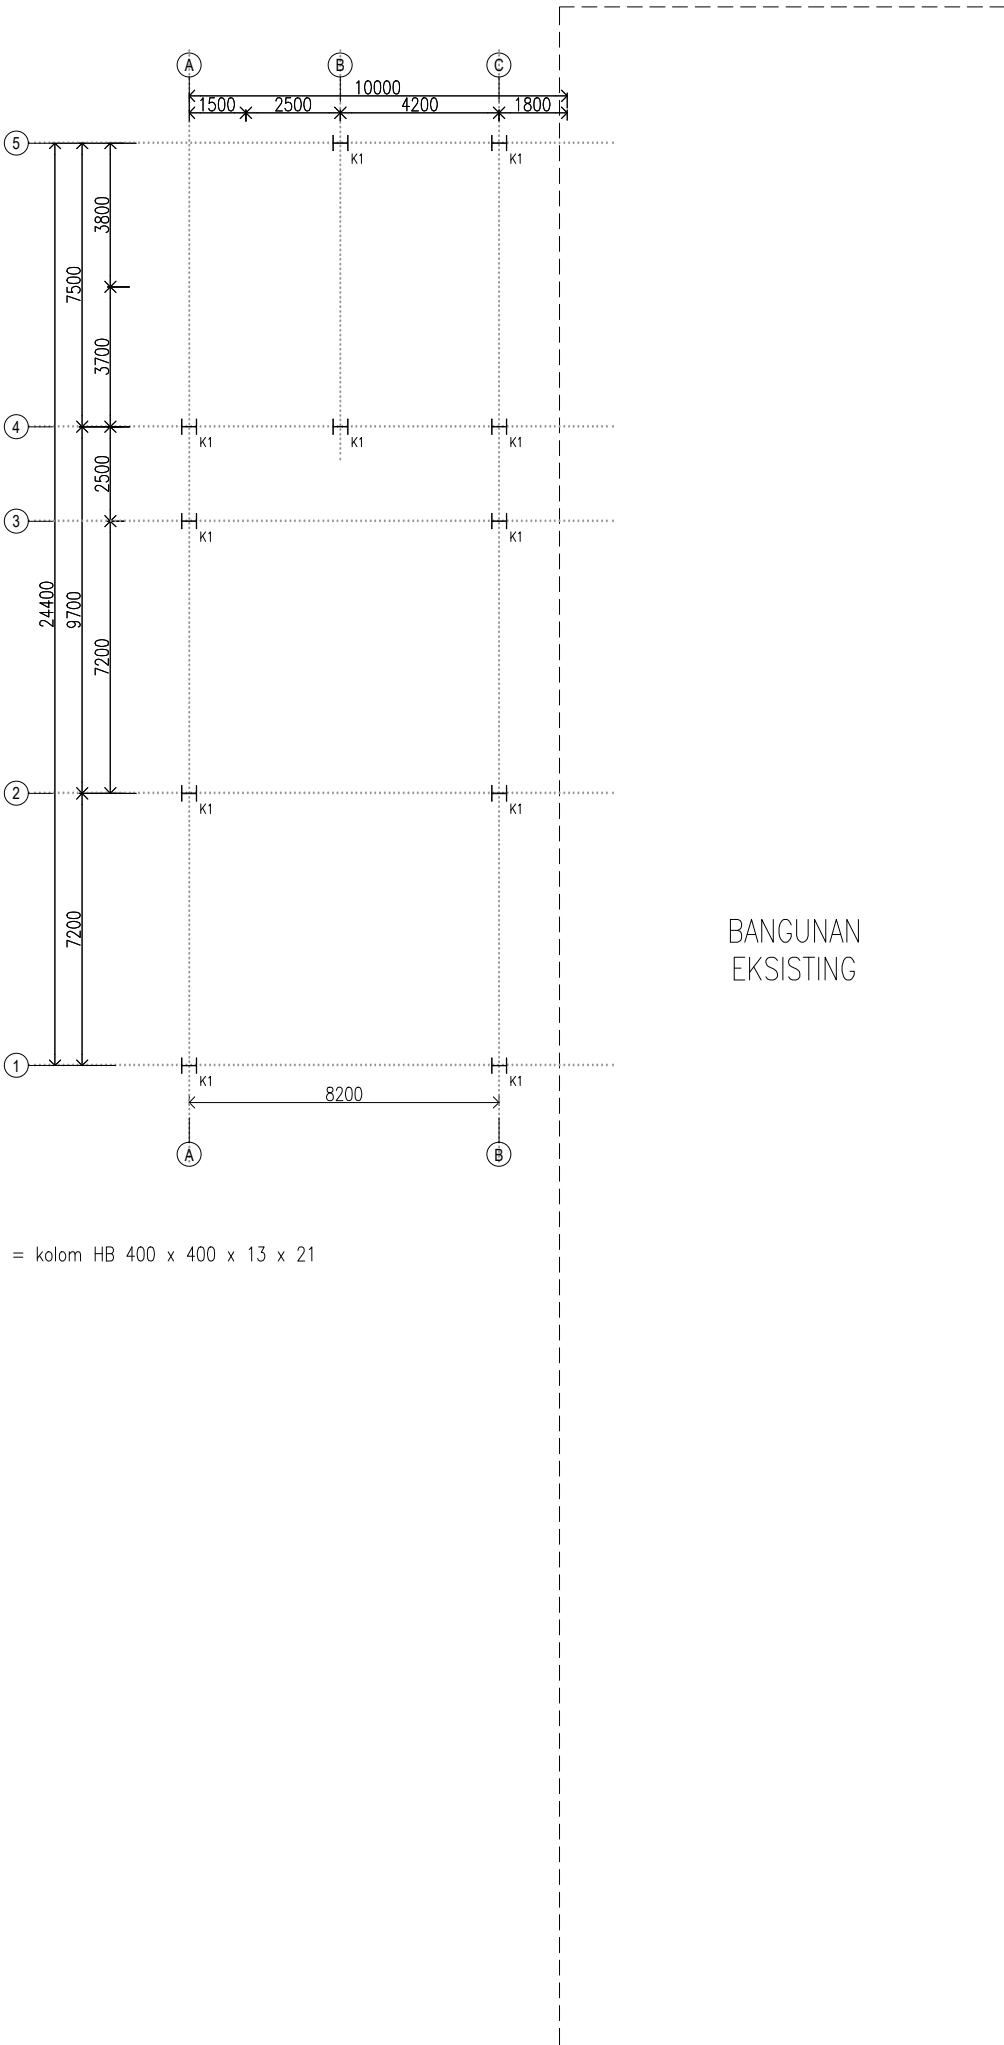

KETERANGAN			
REVISI			
NO.	URAIAN	TANGGAL	PARAF
PEMBERI TUGAS :			
NAMA PROYEK :			
PERENCANAAN DED PRIMAUSADA SUKOREJO			
MENGETAHUI:			
PEMILIK			
KONSULTAN PERENCANA :			
 PT.ASKA MULIA ANOPAMA architecture.interior.and urban design Jl.Prambanan-Piyungan KM.1,5 no.8 Ngoro-Oro, Ringinsari, Bokoharjo, Prambanan, Sleman, Yogyakarta, 55572			
PENANGGUNG JAWAB ARSITEKTUR:			
 AGUS SETIAWAN,ST.,M.Arch.,IAI,GP AHLI ARSITEK—MADYA			
PENANGGUNG JAWAB STRUKTUR:			
 WAHYU HENDRATNO, ST AHLI TEKNIK BANGUNAN GEDUNG—MADYA			
PENANGGUNG JAWAB MEKANIKAL—ELEKTRIKAL—PLUMBING:			
 NOVA NURDIANSYAH, ST AHLI TEKNIK TENAGA LISTRIK—MADYA			
NAMA GAMBAR :			
DENAH KOLOM BAJA			
NO. PROYEK :		TANGGAL :	
—		DIGAMBAR :	
SATUAN UKURAN :		DIPERIKSA :	
		DISETUJUI :	
SKALA	NO. GAMBAR	NO. REVISI	NO. LEMBAR
1:200 PAPER A3	S.4.01		4

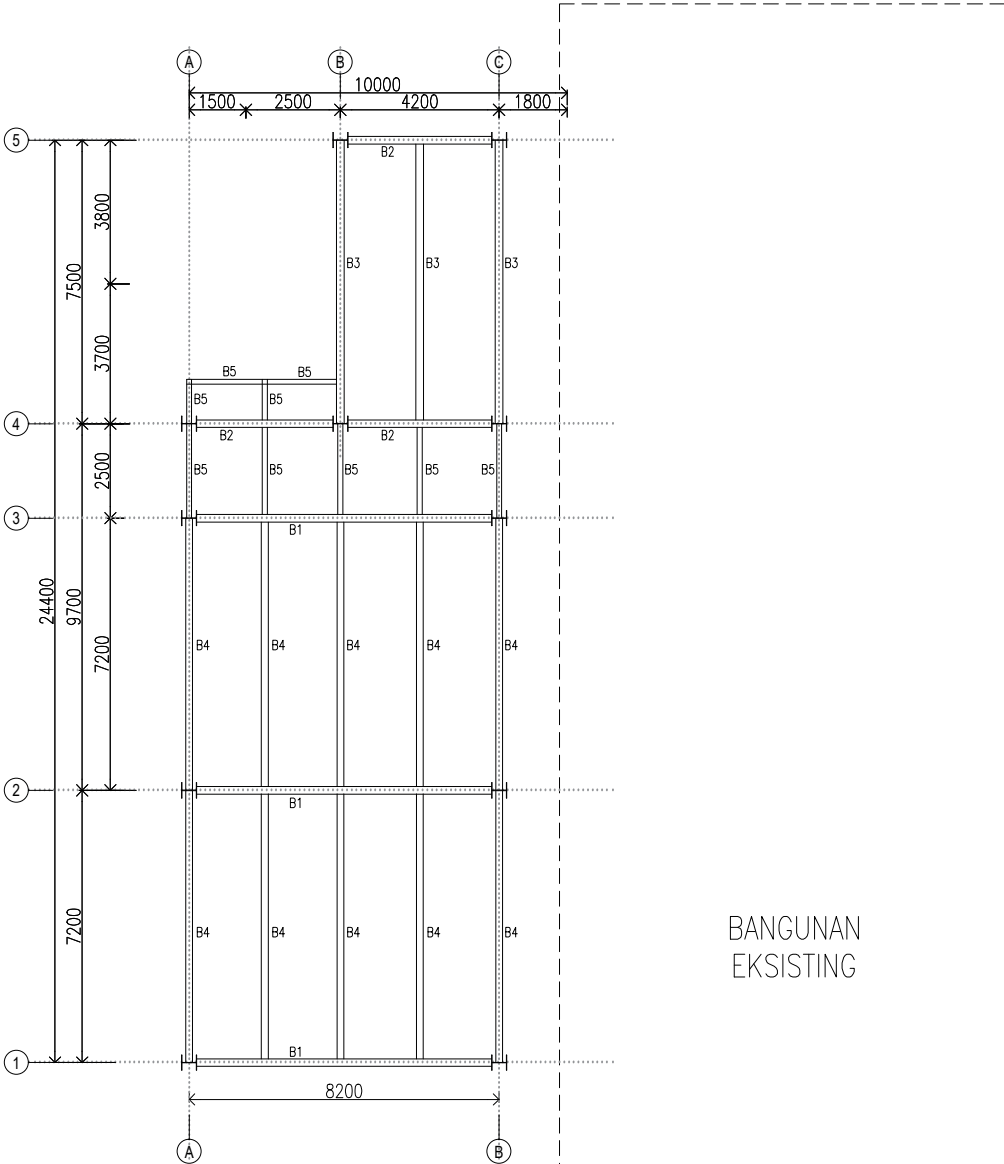



- B1 = balok IWF 500 x 200 x 10 x 16
B2 = balok IWF 450 x 200 x 9 x 14
B3 = balok IWF 400 x 200 x 8 x 13
B4 = balok IWF 350 x 175 x 7 x 11
B5 = balok IWF 250 x 125 x 6 x 9



DENAH BALOK BAJA +4,00


SKALA 1: 200 PAPER A3

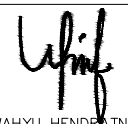KETERANGAN			
REVISI			
NO.	URAIAN	TANGGAL	PARAF
PEMBERI TUGAS :			
NAMA PROYEK :			
PERENCANAAN DED PRIMAUSADA SUKOREJO			
MENGETAHUI:			
PEMILIK			
KONSULTAN PERENCANA :			
 PT.ASKA MULIA ANOPAMA <i>architecture.interior.and urban design</i> Jl.Prambanan-Piyungan KM.1,5 no.8 Ngoro-Oro, Ringinsari, Bokoharjo, Prambanan, Sleman, Yogyakarta, 55572			
PENANGGUNG JAWAB ARSITEKTUR:			
 AGUS SETIAWAN,ST.,M.Arch.,IAI,GP AHLI ARSITEK—MADYA			
PENANGGUNG JAWAB STRUKTUR:			
 WAHYU HENDRATNO, ST AHLI TEKNIK BANGUNAN GEDUNG—MADYA			
PENANGGUNG JAWAB MEKANIKAL—ELEKTRIKAL—PLUMBING:			
 NOVA NURDIANSYAH, ST AHLI TEKNIK TENAGA LISTRIK—MADYA			
NAMA GAMBAR :			
DENAH BALOK BAJA +4.00			
NO. PROYEK :		TANGGAL :	
—		DIGAMBAR :	
SATUAN UKURAN :		DIPERIKSA :	
		DISETUJUI :	
SKALA	NO. GAMBAR	NO. REVISI	NO. LEMBAR
1:200 PAPER A3	S.5.01		5

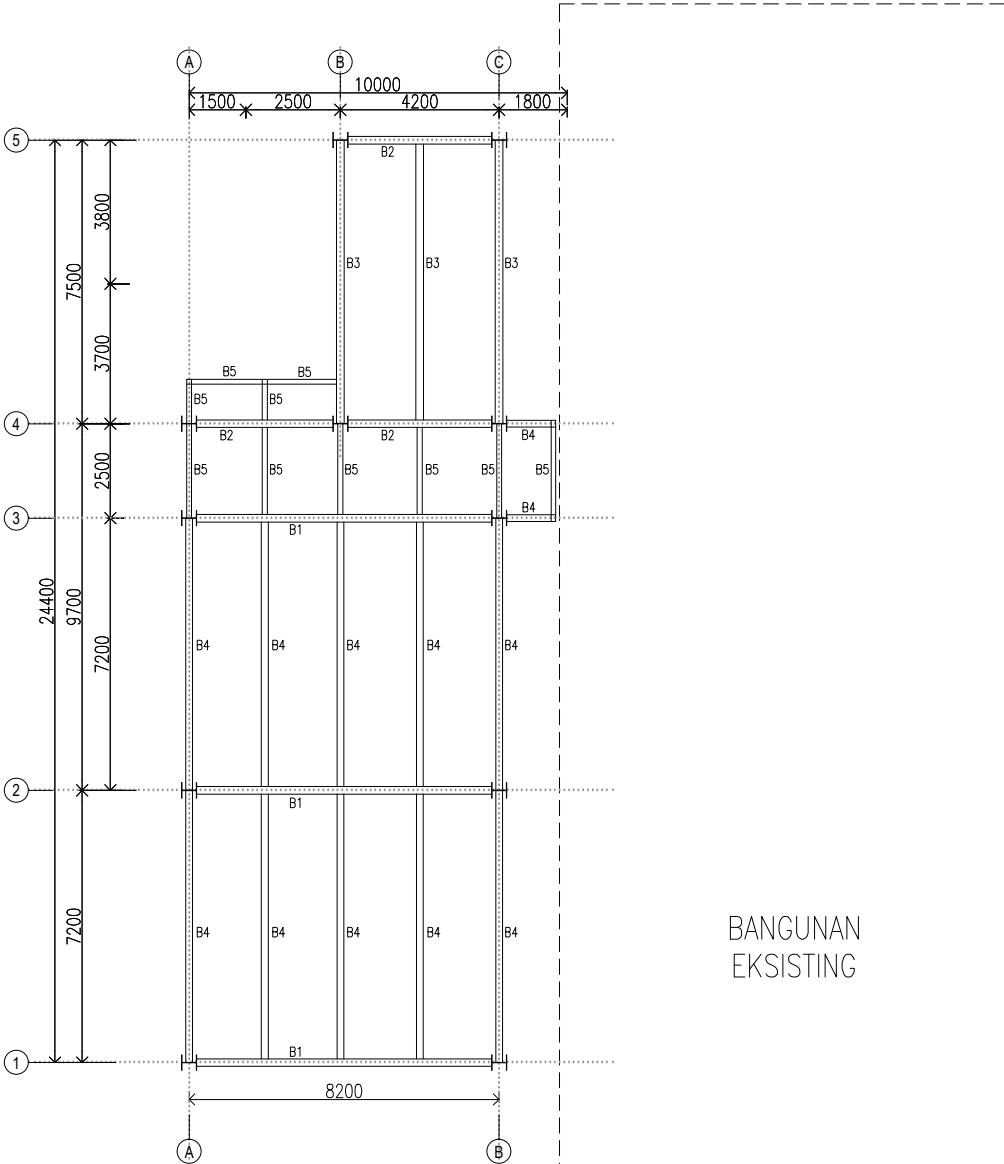

- B1 = balok IWF 500 x 200 x 10 x 16
B2 = balok IWF 450 x 200 x 9 x 14
B3 = balok IWF 400 x 200 x 8 x 13
B4 = balok IWF 350 x 175 x 7 x 11
B5 = balok IWF 250 x 125 x 6 x 9

KETERANGAN			
REVISI			
NO.	URAIAN	TANGGAL	PARAF
PEMBERI TUGAS :			
NAMA PROYEK :			
PERENCANAAN DED PRIMAHUSADA SUKOREJO			
MENGETAHUI:			
PEMILIK			
KONSULTAN PERENCANA :			
PT.ASKA MULIA ANOPAMA architecture.interior.and urban design Jl.Prambanan-Piyungan KM.1,5 no.8 Ngoro-Oro, Ringinsari, Bokoharjo, Prambanan, Sleman, Yogyakarta, 55572			
PENANGGUNG JAWAB ARSITEKTUR:			
AGUS SETIAWAN,ST.,M.Arch.,IAI,GP AHLI ARSITEK-MADYA			
PENANGGUNG JAWAB STRUKTUR:			
WAHYU HENDRATNO, ST AHLI TEKNIK BANGUNAN GEDUNG-MADYA			
PENANGGUNG JAWAB MEKANIKAL-ELEKTRIKAL-PLUMBING:			
NOVA NURDIANSYAH, ST AHLI TEKNIK TENAGA LISTRIK-MADYA			
NAMA GAMBAR :			
DENAH BALOK BAJA +7.85			
NO. PROYEK :		TANGGAL :	
-		DIGAMBAR :	
SATUAN UKURAN :		DIPERIKSA :	
		DISETUJUI :	
SKALA	NO. GAMBAR	NO. REVISI	NO. LEMBAR
1:200 PAPER A3	S.5.02		6

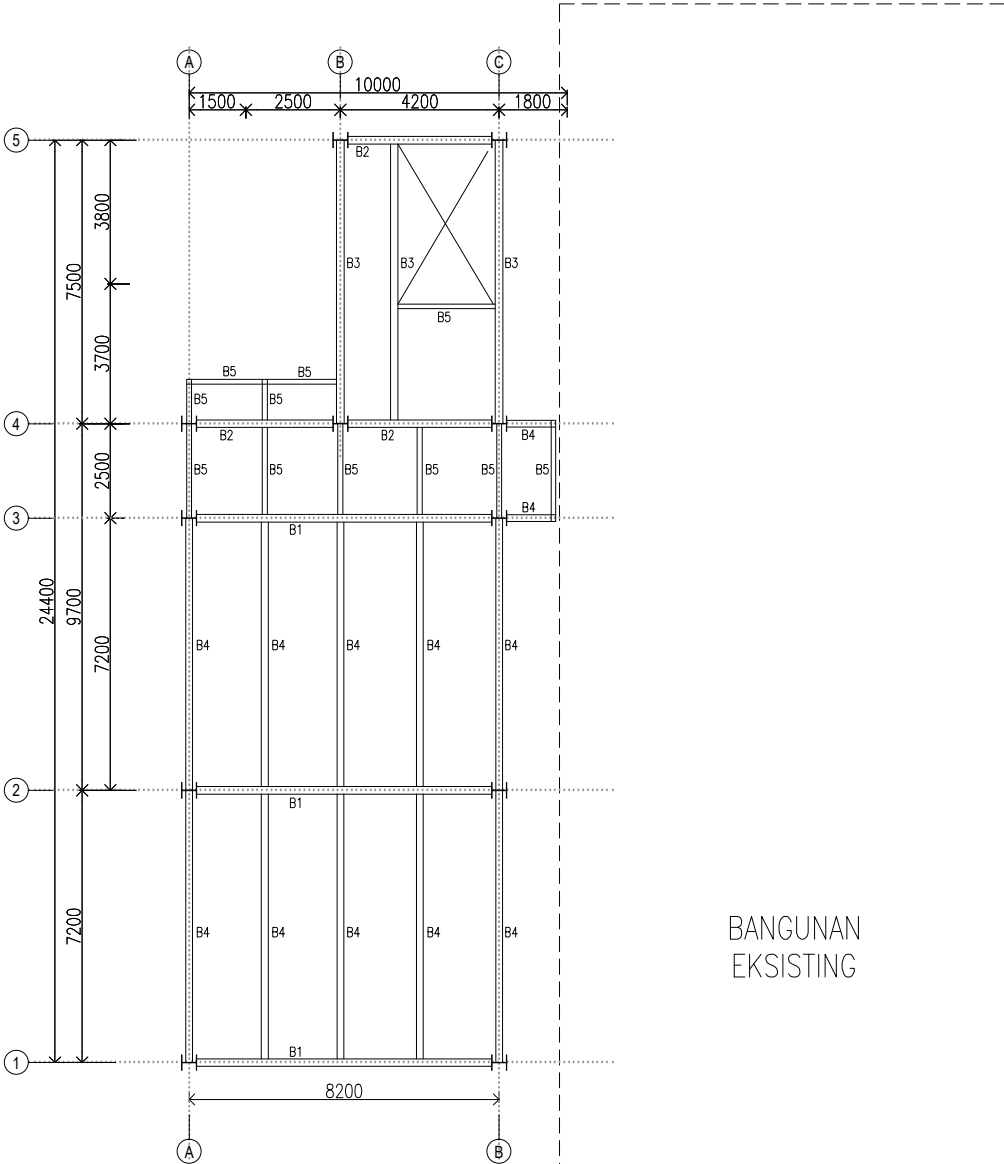


BANGUNAN
EKSISTING


- B1 = balok IWF 500 x 200 x 10 x 16
B2 = balok IWF 450 x 200 x 9 x 14
B3 = balok IWF 400 x 200 x 8 x 13
B4 = balok IWF 350 x 175 x 7 x 11
B5 = balok IWF 250 x 125 x 6 x 9



DENAH BALOK BAJA +11,70


SKALA 1: 200 PAPER A3

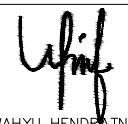KETERANGAN			
REVISI			
NO.	URAIAN	TANGGAL	PARAF
PEMBERI TUGAS :			
NAMA PROYEK :			
PERENCANAAN DED PRIMAHUSADA SUKOREJO			
MENGETAHUI:			
PEMILIK			
KONSULTAN PERENCANA :			
 PT.ASKA MULIA ANOPAMA <i>architecture.interior.and urban design</i> Jl.Prambanan-Piyungan KM.1,5 no.8 Ngoro-Oro, Ringinsari, Bokoharjo, Prambanan, Sleman, Yogyakarta, 55572			
PENANGGUNG JAWAB ARSITEKTUR:			
 AGUS SETIAWAN,ST.,M.Arch.,IAI,GP AHLI ARSITEK—MADYA			
PENANGGUNG JAWAB STRUKTUR:			
 WAHYU HENDRATNO, ST AHLI TEKNIK BANGUNAN GEDUNG—MADYA			
PENANGGUNG JAWAB MEKANIKAL—ELEKTRIKAL—PLUMBING:			
 NOVA NURDIANSYAH, ST AHLI TEKNIK TENAGA LISTRIK—MADYA			
NAMA GAMBAR :			
DENAH BALOK BAJA +11.70			
NO. PROYEK :		TANGGAL :	
—		DIGAMBAR :	
SATUAN UKURAN :		DIPERIKSA :	
		DISETUJUI :	
SKALA	NO. GAMBAR	NO. REVISI	NO. LEMBAR
1:200 PAPER A3	S.5.03		7

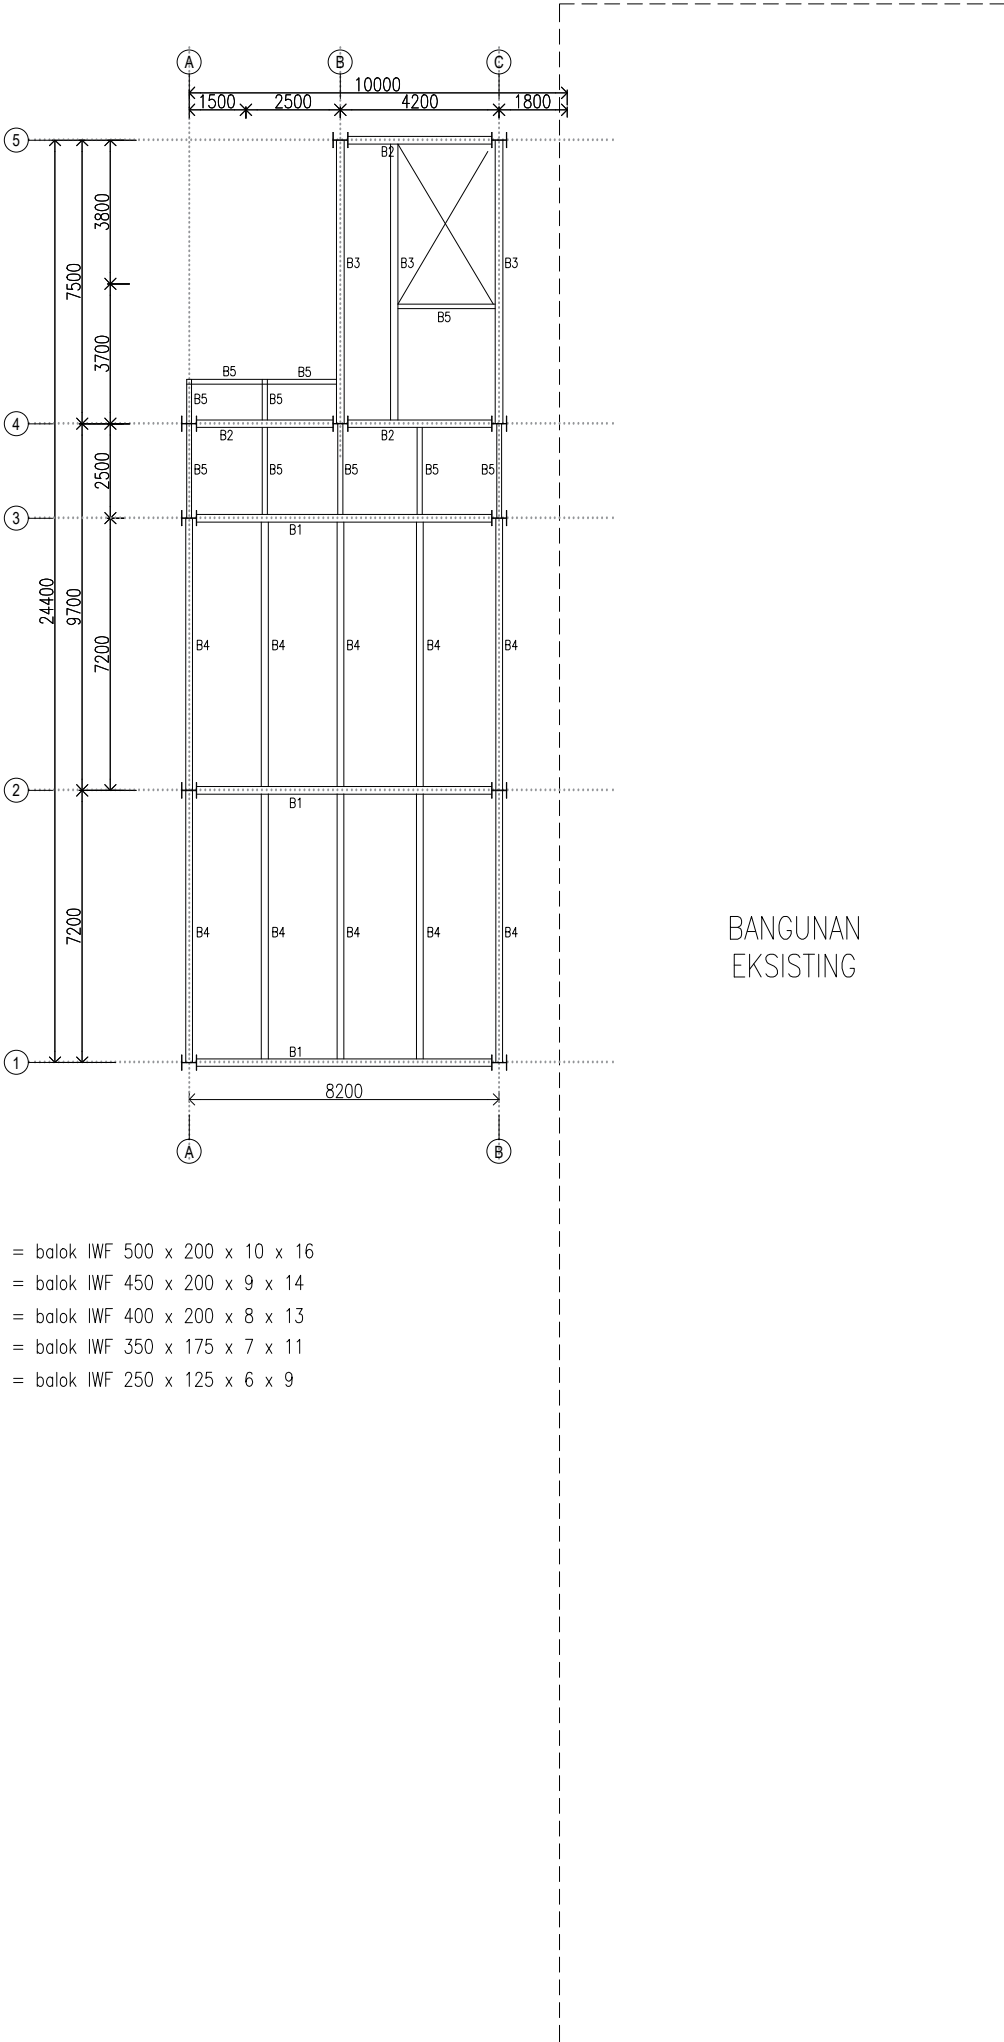


- B1 = balok IWF 500 x 200 x 10 x 16
B2 = balok IWF 450 x 200 x 9 x 14
B3 = balok IWF 400 x 200 x 8 x 13
B4 = balok IWF 350 x 175 x 7 x 11
B5 = balok IWF 250 x 125 x 6 x 9

KETERANGAN			
REVISI			
NO.	URAIAN	TANGGAL	PARAF
PEMBERI TUGAS :			
NAMA PROYEK :			
PERENCANAAN DED PRIMAUSADA SUKOREJO			
MENGETAHUI:			
PEMILIK			
KONSULTAN PERENCANA :			
PT.ASKA MULIA ANOPAMA architecture.interior.and urban design Jl.Prambanan-Piyungan KM.1,5 no.8 Ngoro-Oro, Ringinsari, Bokoharjo, Prambanan, Sleman, Yogyakarta, 55572			
PENANGGUNG JAWAB ARSITEKTUR:			
AGUS SETIAWAN,ST.,M.Arch.,IAI,GP AHLI ARSITEK-MADYA			
PENANGGUNG JAWAB STRUKTUR:			
WAHYU HENDRATNO, ST AHLI TEKNIK BANGUNAN GEDUNG-MADYA			
PENANGGUNG JAWAB MEKANIKAL-ELEKTRIKAL-PLUMBING:			
NOVA NURDIANSYAH, ST AHLI TEKNIK TENAGA LISTRIK-MADYA			
NAMA GAMBAR :			
DENAH BALOK BAJA +15.55			
NO. PROYEK :		TANGGAL :	
-		DIGAMBAR :	
SATUAN UKURAN :		DIPERIKSA :	
		DISETUJUI :	
SKALA	NO. GAMBAR	NO. REVISI	NO. LEMBAR
1:200 PAPER A3	S.5.04		8

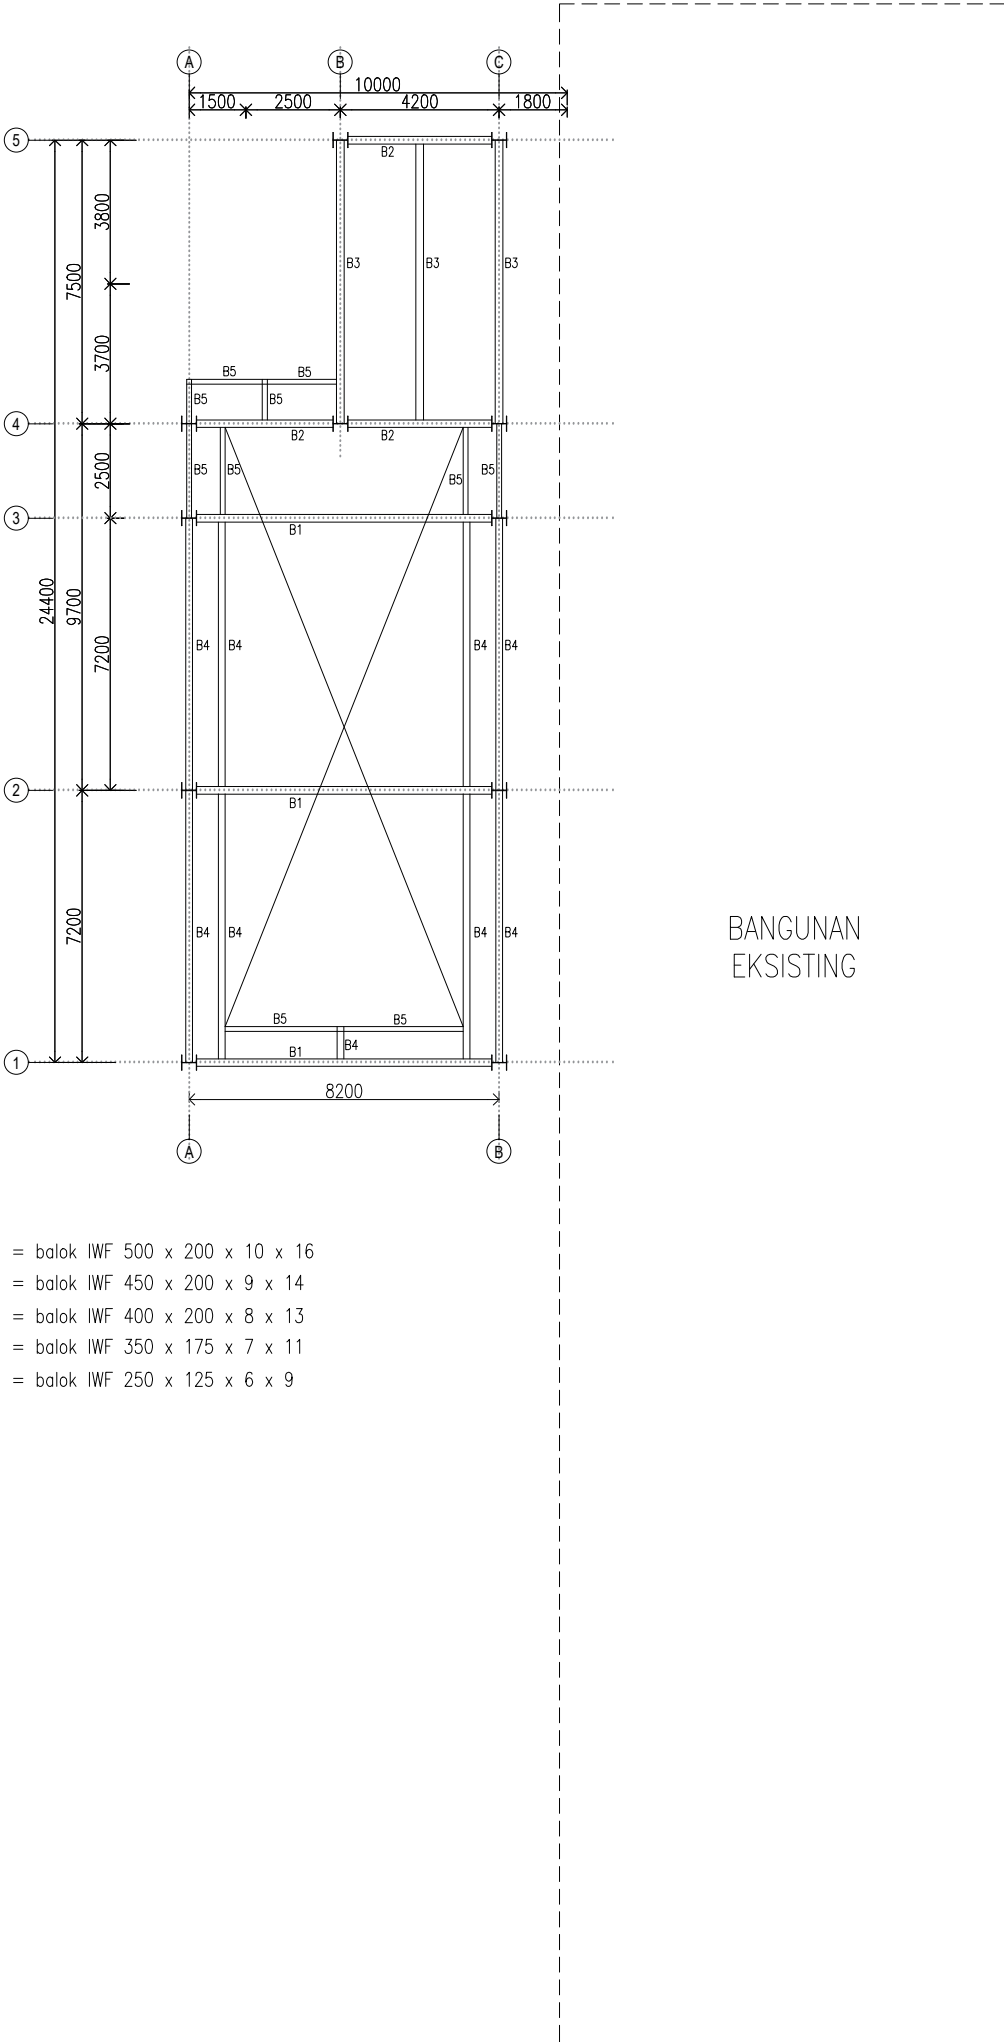


- B1 = balok IWF 500 x 200 x 10 x 16
B2 = balok IWF 450 x 200 x 9 x 14
B3 = balok IWF 400 x 200 x 8 x 13
B4 = balok IWF 350 x 175 x 7 x 11
B5 = balok IWF 250 x 125 x 6 x 9

KETERANGAN			
REVISI			
NO.	URAIAN	TANGGAL	PARAF
PEMBERI TUGAS :			
NAMA PROYEK :			
PERENCANAAN DED PRIMAHUSADA SUKOREJO			
MENGETAHUI:			
PEMILIK			
KONSULTAN PERENCANA :			
 PT. ASKA MULIA ANOPAMA architecture, interior, and urban design Jl. Prambanan-Piyungan KM. 1,5 no.8 Ngoro-Oro, Ringinsari, Bokoharjo, Prambanan, Sleman, Yogyakarta, 55572			
PENANGGUNG JAWAB ARSITEKTUR:			
 AGUS SETIAWAN, ST., M. Arch., IAI, GP AHLI ARSITEK – MADYA			
PENANGGUNG JAWAB STRUKTUR:			
 WAHYU HENDRATNO, ST AHLI TEKNIK BANGUNAN GEDUNG – MADYA			
PENANGGUNG JAWAB MEKANIKAL – ELEKTRIKAL – PLUMBING:			
 NOVA NURDIANSYAH, ST AHLI TEKNIK TENAGA LISTRIK – MADYA			
NAMA GAMBAR :			
DENAH BALOK BAJA +19.40			
NO. PROYEK :		TANGGAL :	
-		DIGAMBAR :	
SATUAN UKURAN :		DIPERIKSA :	
		DISETUJUI :	
SKALA	NO. GAMBAR	NO. REVISI	NO. LEMBAR
1:200 PAPER A3	S.5.05		9

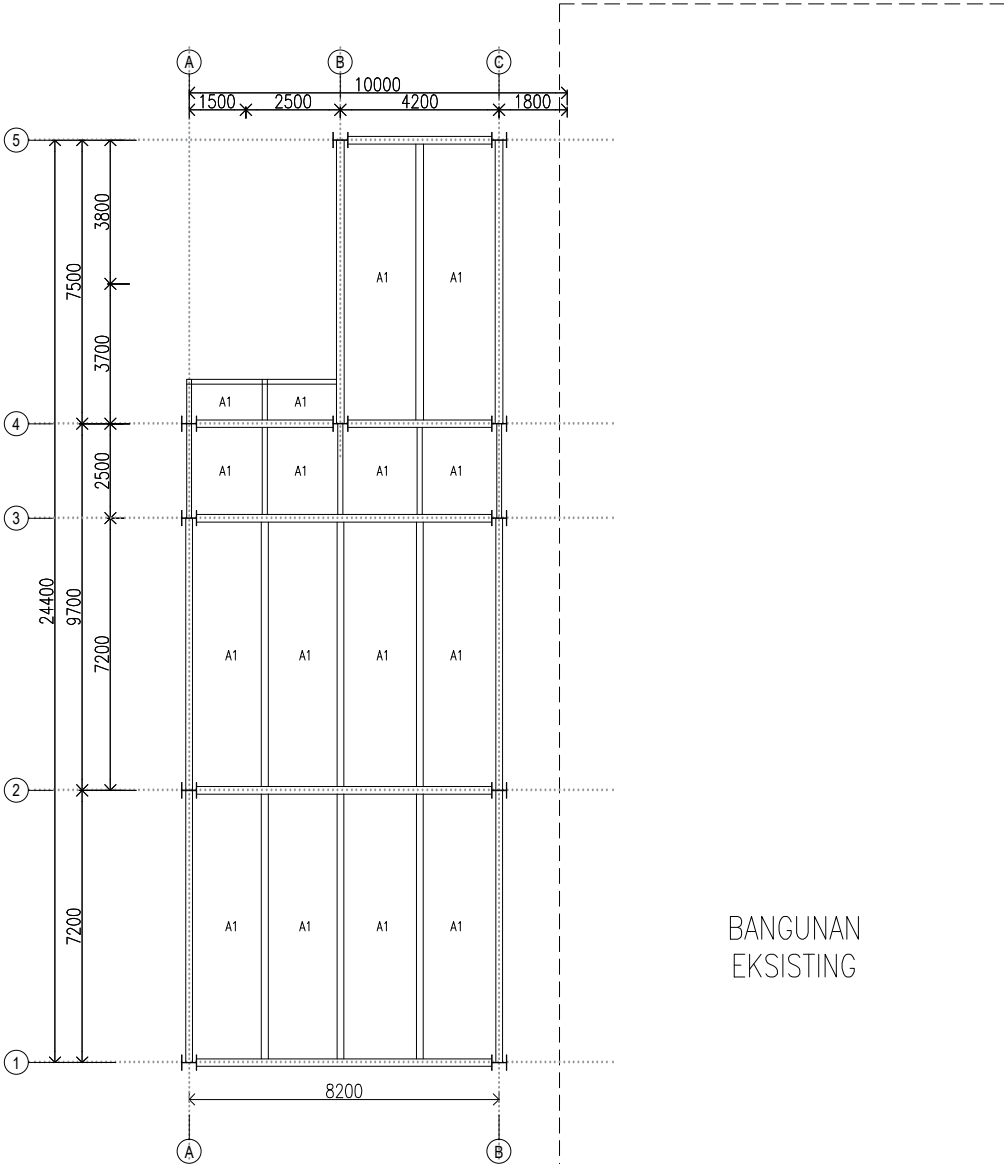

- B1 = balok IWF 500 x 200 x 10 x 16
B2 = balok IWF 450 x 200 x 9 x 14
B3 = balok IWF 400 x 200 x 8 x 13
B4 = balok IWF 350 x 175 x 7 x 11
B5 = balok IWF 250 x 125 x 6 x 9

KETERANGAN			
REVISI			
NO.	URAIAN	TANGGAL	PARAF
PEMBERI TUGAS :			
NAMA PROYEK :			
PERENCANAAN DED PRIMAHUSADA SUKOREJO			
MENGETAHUI:			
PEMILIK			
KONSULTAN PERENCANA :			
PT.ASKA MULIA ANOPAMA architecture.interior.and urban design Jl.Prambanan-Piyungan KM.1,5 no.8 Ngoro-Oro, Ringinsari, Bokoharjo, Prambanan, Sleman, Yogyakarta, 55572			
PENANGGUNG JAWAB ARSITEKTUR:			
AGUS SETIAWAN,ST.,M.Arch.,IAI,GP AHLI ARSITEK—MADYA			
PENANGGUNG JAWAB STRUKTUR:			
WAHYU HENDRATNO, ST AHLI TEKNIK BANGUNAN GEDUNG—MADYA			
PENANGGUNG JAWAB MEKANIKAL—ELEKTRIKAL—PLUMBING:			
NOVA NURDIANSYAH, ST AHLI TEKNIK TENAGA LISTRIK—MADYA			
NAMA GAMBAR :			
DENAH PLAT LANTAI +4.15			
NO. PROYEK :		TANGGAL :	
—		DIGAMBAR :	
SATUAN UKURAN :		DIPERIKSA :	
		DISETUJUI :	
SKALA	NO. GAMBAR	NO. REVISI	NO. LEMBAR
1:200 PAPER A3	S.6.01		10

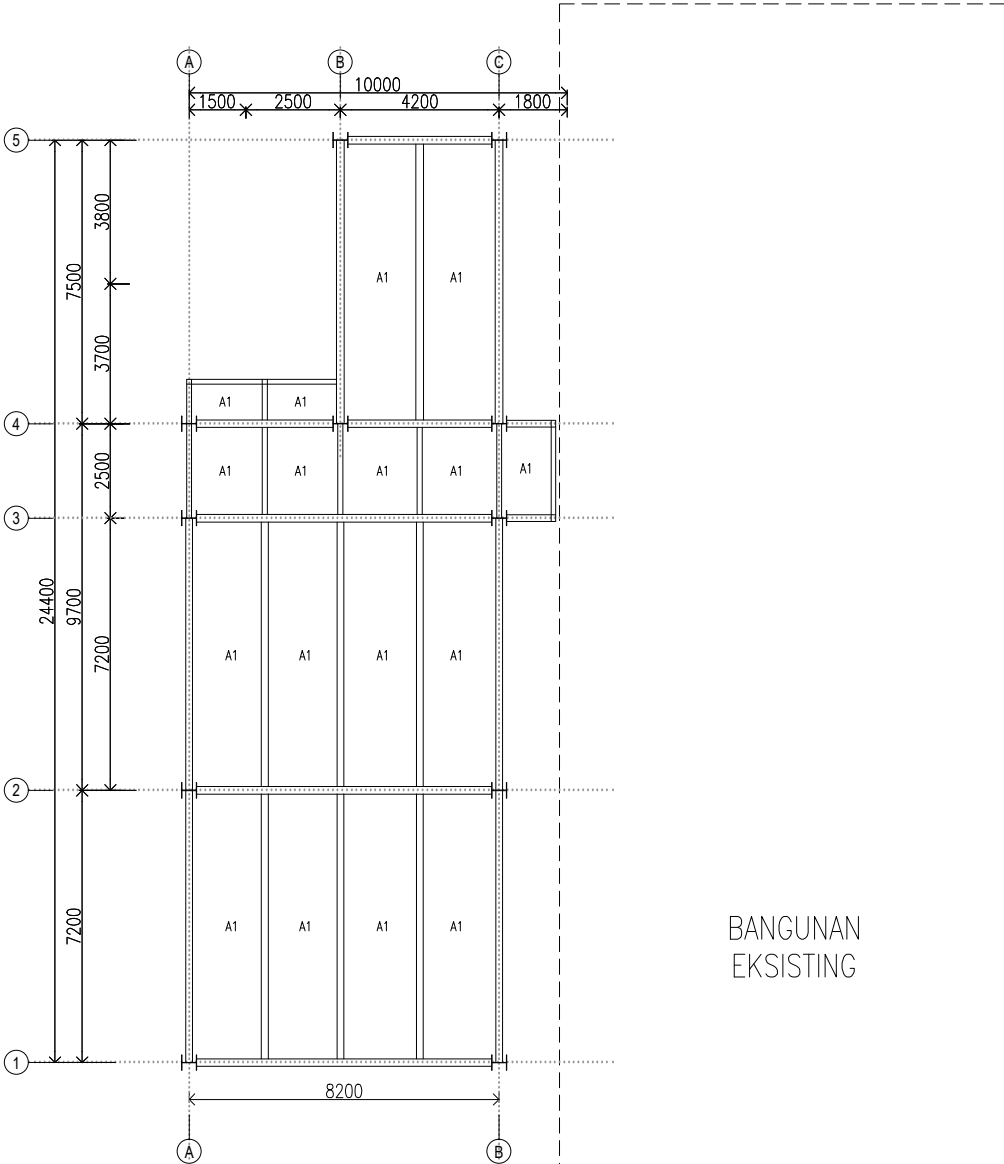

- B1 = balok IWF 500 x 200 x 10 x 16
B2 = balok IWF 450 x 200 x 9 x 14
B3 = balok IWF 400 x 200 x 8 x 13
B4 = balok IWF 350 x 175 x 7 x 11
B5 = balok IWF 250 x 125 x 6 x 9


BANGUNAN
EKSISTING



DENAH PLAT LANTAI +8,00

SKALA 1: 200 PAPER A3

KETERANGAN			
REVISI			
NO.	URAIAN	TANGGAL	PARAF
PEMBERI TUGAS :			
NAMA PROYEK :			
PERENCANAAN DED PRIMAHUSADA SUKOREJO			
MENGETAHUI:			
PEMILIK			
KONSULTAN PERENCANA :			
 PT. ASKA MULIA ANOPAMA <i>architecture, interior, and urban design</i> Jl. Prambanan-Piyungan KM. 1,5 no.8 Ngoro-Oro, Ringinsari, Bokoharjo, Prambanan, Sleman, Yogyakarta, 55572			
PENANGGUNG JAWAB ARSITEKTUR:			
 AGUS SETIAWAN, ST., M. Arch., IAI, GP AHLI ARSITEK – MADYA			
PENANGGUNG JAWAB STRUKTUR:			
 WAHYU HENDRATNO, ST AHLI TEKNIK BANGUNAN GEDUNG – MADYA			
PENANGGUNG JAWAB MEKANIKAL – ELEKTRIKAL – PLUMBING:			
 NOVA NURDIANSYAH, ST AHLI TEKNIK TENAGA LISTRIK – MADYA			
NAMA GAMBAR :			
DENAH PLAT LANTAI +8.00			
NO. PROYEK :		TANGGAL :	
-		DIGAMBAR :	
SATUAN UKURAN :		DIPERIKSA :	
		DISETUJUI :	
SKALA	NO. GAMBAR	NO. REVISI	NO. LEMBAR
1:200 PAPER A3	S.6.02		11

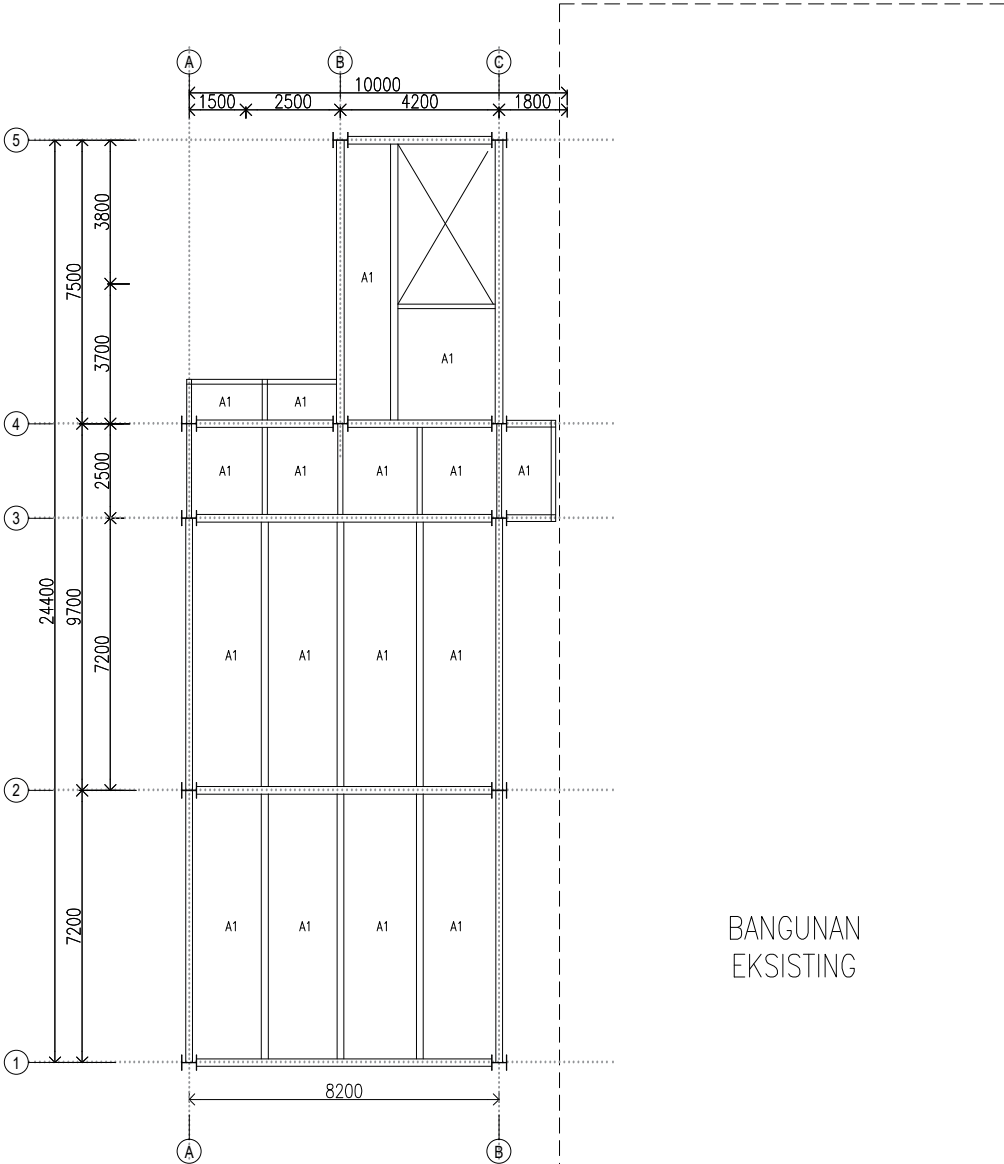


- B1 = balok IWF 500 x 200 x 10 x 16
B2 = balok IWF 450 x 200 x 9 x 14
B3 = balok IWF 400 x 200 x 8 x 13
B4 = balok IWF 350 x 175 x 7 x 11
B5 = balok IWF 250 x 125 x 6 x 9


BANGUNAN
EKSISTING



DENAH PLAT LANTAI +11,85

SKALA 1: 200 PAPER A3

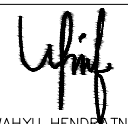KETERANGAN			
REVISI			
NO.	URAIAN	TANGGAL	PARAF
PEMBERI TUGAS :			
NAMA PROYEK :			
PERENCANAAN DED PRIMAHUSADA SUKOREJO			
MENGETAHUI:			
PEMILIK			
KONSULTAN PERENCANA :			
 PT. ASKA MULIA ANOPAMA architecture, interior, and urban design Jl. Prambanan-Piyungan KM. 1,5 no.8 Ngoro-Oro, Ringinsari, Bokoharjo, Prambanan, Sleman, Yogyakarta, 55572			
PENANGGUNG JAWAB ARSITEKTUR:			
 AGUS SETIAWAN, ST., M. Arch., IAI, GP AHLI ARSITEK – MADYA			
PENANGGUNG JAWAB STRUKTUR:			
 WAHYU HENDRATNO, ST AHLI TEKNIK BANGUNAN GEDUNG – MADYA			
PENANGGUNG JAWAB MEKANIKAL – ELEKTRIKAL – PLUMBING:			
 NOVA NURDIANSYAH, ST AHLI TEKNIK TENAGA LISTRIK – MADYA			
NAMA GAMBAR :			
DENAH PLAT LANTAI +11.85			
NO. PROYEK :		TANGGAL :	
-		DIGAMBAR :	
SATUAN UKURAN :		DIPERIKSA :	
		DISETUJUI :	
SKALA	NO. GAMBAR	NO. REVISI	NO. LEMBAR
1:200 PAPER A3	S.6.03		12

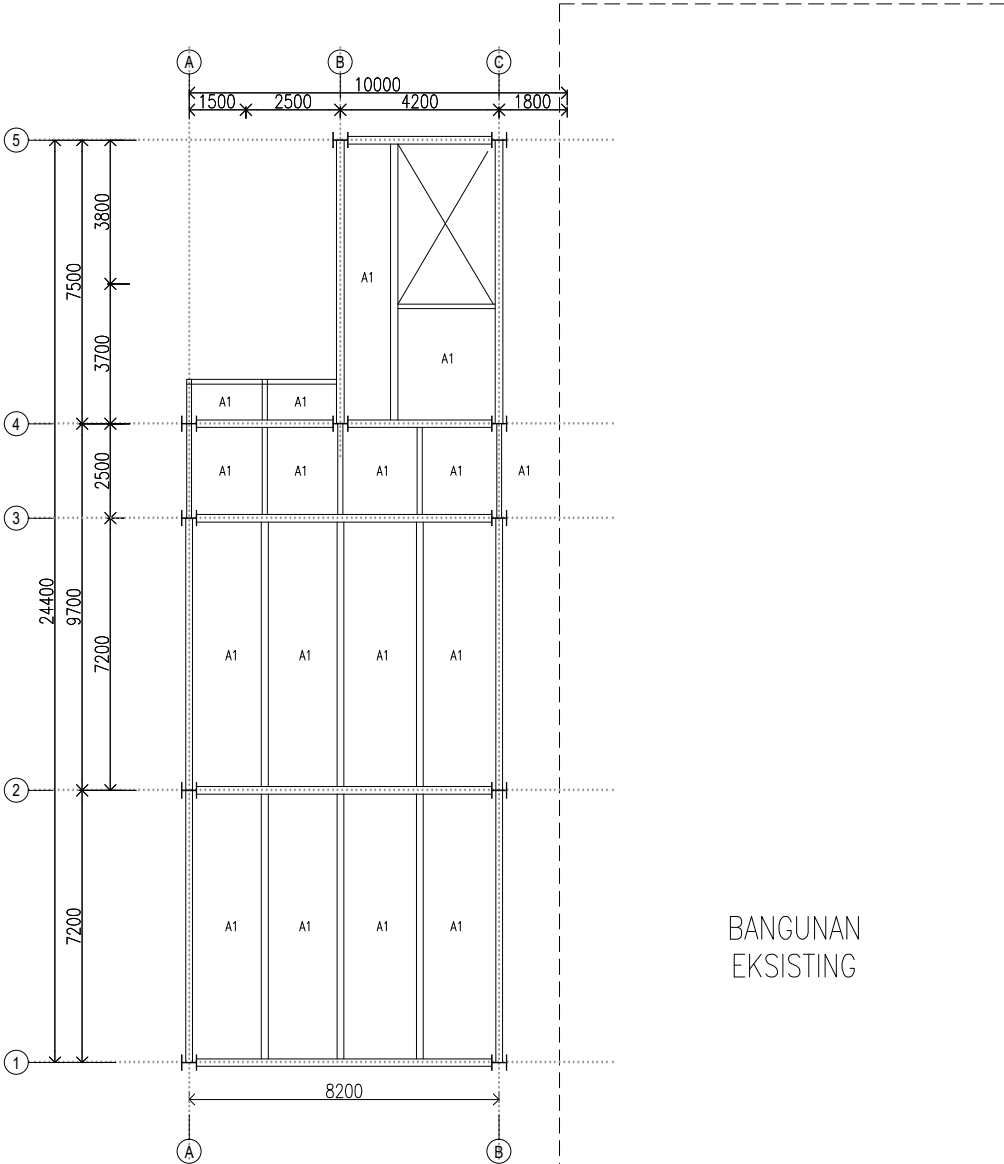

- B1 = balok IWF 500 x 200 x 10 x 16
B2 = balok IWF 450 x 200 x 9 x 14
B3 = balok IWF 400 x 200 x 8 x 13
B4 = balok IWF 350 x 175 x 7 x 11
B5 = balok IWF 250 x 125 x 6 x 9


BANGUNAN
EKSISTING



DENAH PLAT LANTAI +15,70

SKALA 1: 200 PAPER A3


KETERANGAN			
REVISI			
NO.	URAIAN	TANGGAL	PARAF
PEMBERI TUGAS :			
NAMA PROYEK :			
PERENCANAAN DED PRIMAHUSADA SUKOREJO			
MENGETAHUI:			
PEMILIK			
KONSULTAN PERENCANA :			
 PT.ASKA MULIA ANOPAMA <i>architecture.interior.and urban design</i> Jl.Prambanan-Piyungan KM.1,5 no.8 Ngoro-Oro, Ringinsari, Bokoharjo, Prambanan, Sleman, Yogyakarta, 55572			
PENANGGUNG JAWAB ARSITEKTUR:			
 AGUS SETIAWAN,ST.,M.Arch.,IAI,GP AHLI ARSITEK—MADYA			
PENANGGUNG JAWAB STRUKTUR:			
 WAHYU HENDRATNO, ST AHLI TEKNIK BANGUNAN GEDUNG—MADYA			
PENANGGUNG JAWAB MEKANIKAL—ELEKTRIKAL—PLUMBING:			
 NOVA NURDIANSYAH, ST AHLI TEKNIK TENAGA LISTRIK—MADYA			
NAMA GAMBAR :			
DENAH PELAT LANTAI +15.70			
NO. PROYEK :		TANGGAL :	
—		DIGAMBAR :	
SATUAN UKURAN :		DIPERIKSA :	
		DISETUJUI :	
SKALA	NO. GAMBAR	NO. REVISI	NO. LEMBAR
1:200 PAPER A3	S.6.04		13

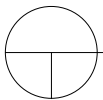

DENAH PLAT LANTAI +19,55

SKALA 1: 200 PAPER A3

- B1 = balok IWF 500 x 200 x 10 x 16
B2 = balok IWF 450 x 200 x 9 x 14
B3 = balok IWF 400 x 200 x 8 x 13
B4 = balok IWF 350 x 175 x 7 x 11
B5 = balok IWF 250 x 125 x 6 x 9

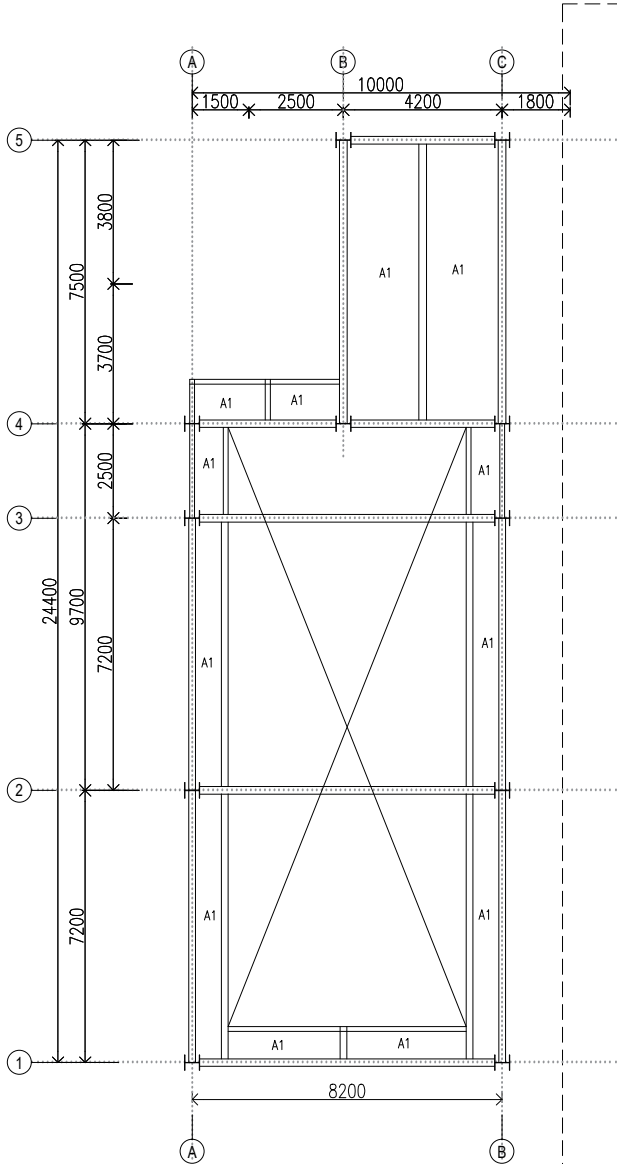

BANGUNAN
EKSISTING

KETERANGAN

REVISI

NO.	URAIAN	TANGGAL	PARAF

PEMBERI TUGAS :

NAMA PROYEK :

PERENCANAAN DED
PRIMAHUSADA SUKOREJO

MENGETAHUI:

PEMILIK

KONSULTAN PERENCANA :



PT. ASKA MULIA ANOPAMA
architecture, interior, and urban design
Jl. Prambanan-Piyungan KM. 1,5 no.8
Ngoro-Oro, Ringinsari, Bokoharjo,
Prambanan, Sleman, Yogyakarta, 55572

PENANGGUNG JAWAB ARSITEKTUR:


AGUS SETIAWAN, ST., M. Arch., IAI, GP
AHLI ARSITEK – MADYA

PENANGGUNG JAWAB STRUKTUR:


WAHYU HENDRATNO, ST
AHLI TEKNIK BANGUNAN GEDUNG – MADYA


PENANGGUNG JAWAB MEKANIKAL – ELEKTRIKAL – PLUMBING:


NOVA NURDIANSYAH, ST
AHLI TEKNIK TENAGA LISTRIK – MADYA

NAMA GAMBAR :

DENAH PLAT LANTAI +19.55


NO. PROYEK :		TANGGAL :	
—		DIGAMBAR :	
SATUAN UKURAN :		DIPERIKSA :	
		DISETUJUI :	
SKALA	NO. GAMBAR	NO. REVISI	NO. LEMBAR
1:200 PAPER A3	S.6.05		14


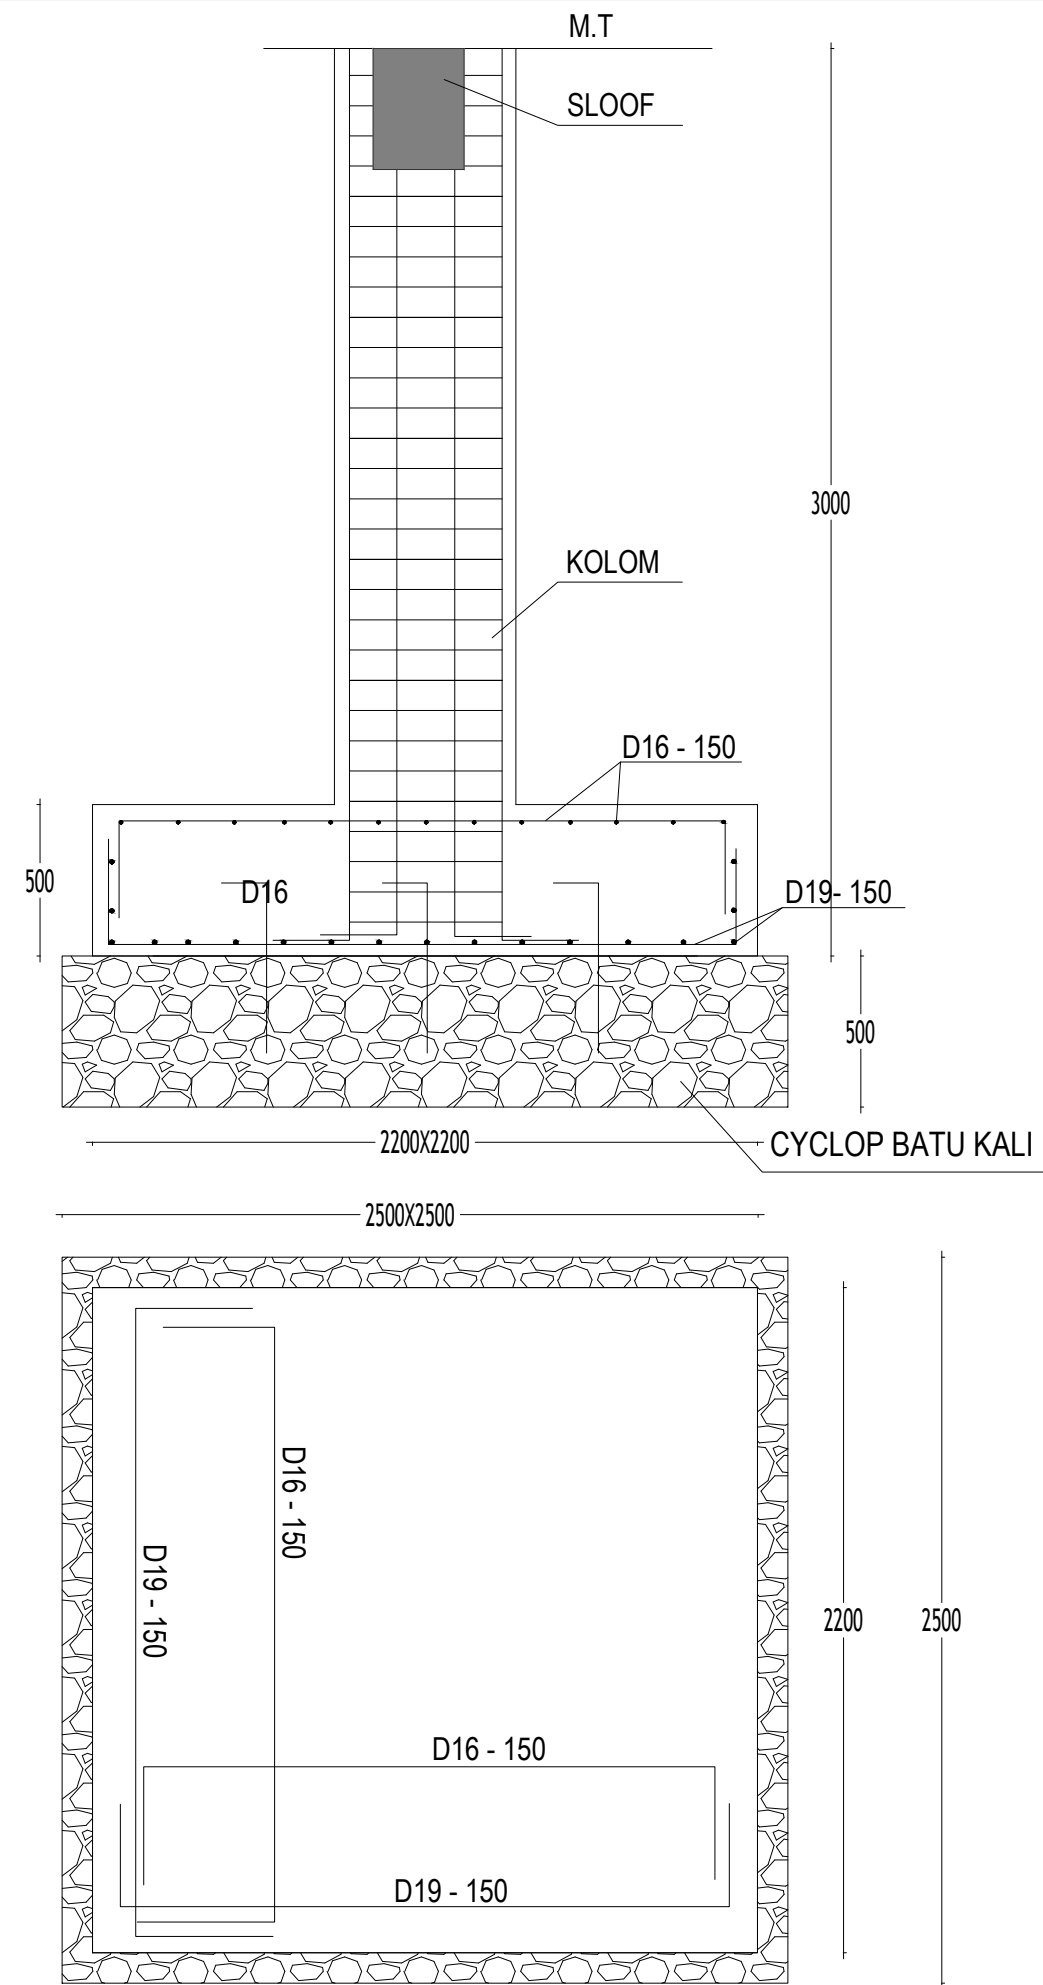


DETAIL FONDASI F1



DETAIL STRUKTUR
SKALA 1:25 PAPER A3

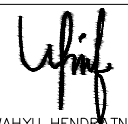
KETERANGAN			
REVISI			
NO.	URAIAN	TANGGAL	PARAF
PEMBERI TUGAS :			
NAMA PROYEK :			
PERENCANAAN DED PRIMAHUSADA SUKOREJO			
MENGETAHUI:			
PEMILIK			
KONSULTAN PERENCANA :			
 PT.ASKA MULIA ANOPAMA <i>architecture.interior.and urban design</i> Jl.Prambanan-Piyungan KM.1,5 no.8 Ngoro-Oro, Ringinsari, Bokoharjo, Prambanan, Sleman, Yogyakarta, 55572			
PENANGGUNG JAWAB ARSITEKTUR:			
 AGUS SETIAWAN,ST.,M.Arch.,IAI,GP AHLI ARSITEK—MADYA			
PENANGGUNG JAWAB STRUKTUR:			
 WAHYU HENDRATNO, ST AHLI TEKNIK BANGUNAN GEDUNG—MADYA			
PENANGGUNG JAWAB MEKANIKAL—ELEKTRIKAL—PLUMBING:			
 NOVA NURDIANSYAH, ST AHLI TEKNIK TENAGA LISTRIK—MADYA			
NAMA GAMBAR :			
DETAIL STRUKTUR			
NO. PROYEK :		TANGGAL :	
—		DIGAMBAR :	
SATUAN UKURAN :		DIPERIKSA :	
		DISETUJUI :	
SKALA	NO. GAMBAR	NO. REVISI	NO. LEMBAR
1:25 PAPER A3	S.7.01		15

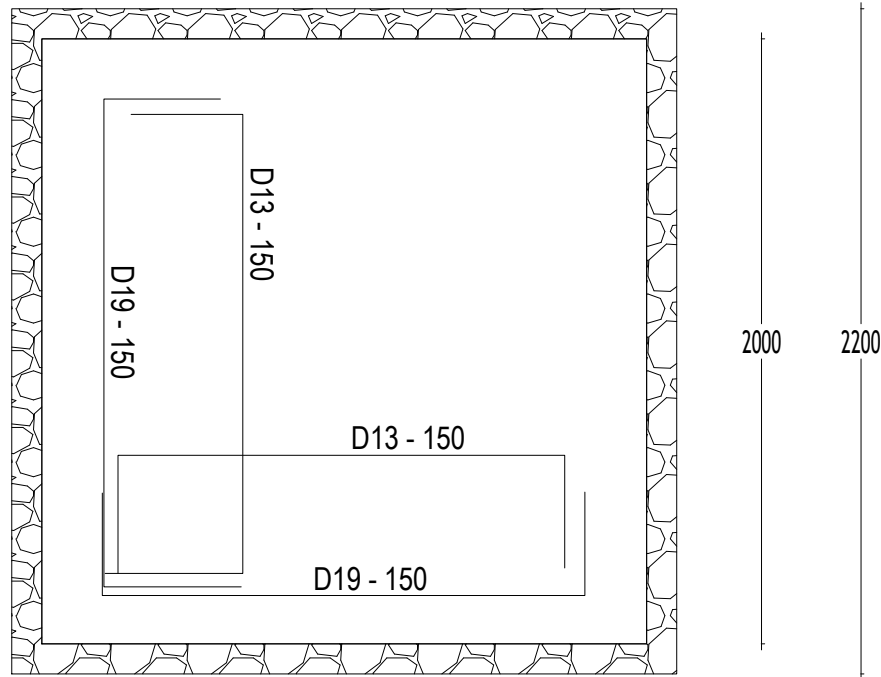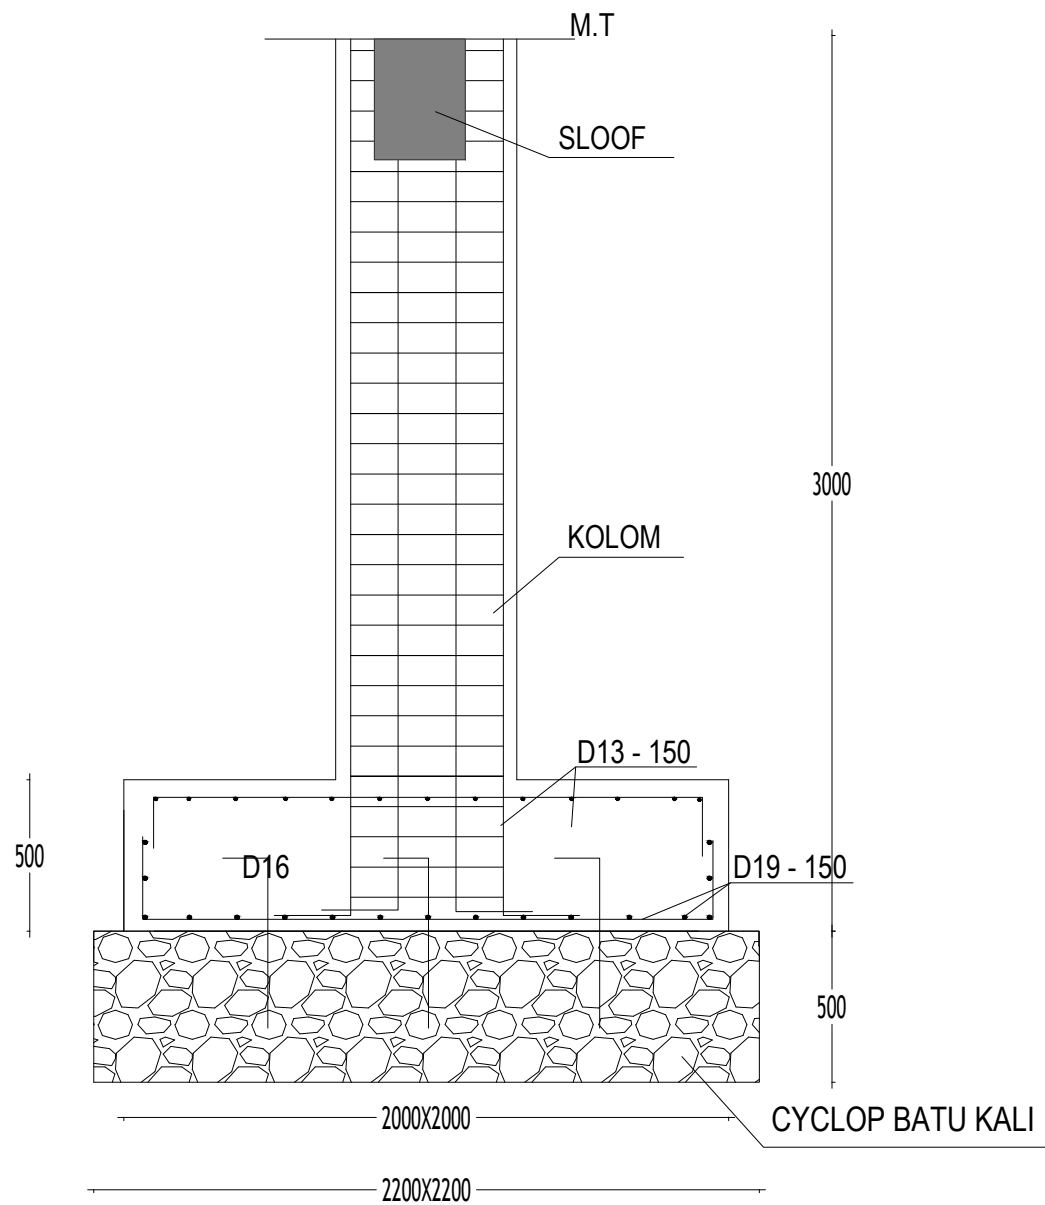



DETAIL FONDASI F2

DETAIL STRUKTUR




SKALA 1:25 PAPER A3



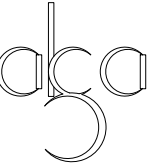
KETERANGAN			
REVISI			
NO.	URAIAN	TANGGAL	PARAF
PEMBERI TUGAS :			
NAMA PROYEK :			
PERENCANAAN DED PRIMAHUSADA SUKOREJO			
MENGETAHUI:			
PEMILIK			
KONSULTAN PERENCANA :			
 PT.ASKA MULIA ANOPAMA <i>architecture.interior.and urban design</i> Jl.Prambanan-Piyungan KM.1,5 no.8 Ngoro-Oro, Ringinsari, Bokoharjo, Prambanan, Sleman, Yogyakarta, 55572			
PENANGGUNG JAWAB ARSITEKTUR:			
 AGUS SETIAWAN,ST.,M.Arch.,IAI,GP AHLI ARSITEK—MADYA			
PENANGGUNG JAWAB STRUKTUR:			
 WAHYU HENDRATNO, ST AHLI TEKNIK BANGUNAN GEDUNG—MADYA			
PENANGGUNG JAWAB MEKANIKAL—ELEKTRIKAL—PLUMBING:			
 NOVA NURDIANSYAH, ST AHLI TEKNIK TENAGA LISTRIK—MADYA			
NAMA GAMBAR :			
DETAIL STRUKTUR			
NO. PROYEK :		TANGGAL :	
—		DIGAMBAR :	
SATUAN UKURAN :		DIPERIKSA :	
		DISETUJUI :	
SKALA	NO. GAMBAR	NO. REVISI	NO. LEMBAR
1:25 PAPER A3	S.7.02		16

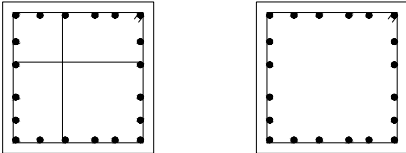
KOLOM LANTAI	KOLOM K1	
	TUMPUAN	LAPANGAN
		
TUL. UTAMA	20 D19	20 D19
SENGKANG	1,5 D10–100	D10–150
DIMENSI	500 X 500	

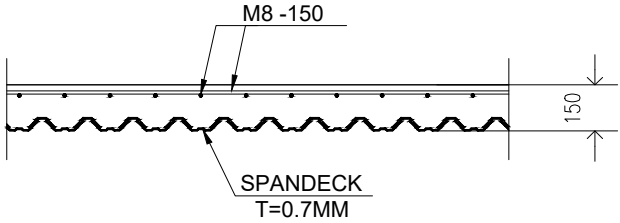

DETIL PLAT METAL DECK
SKALA 1 : 25

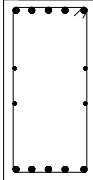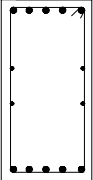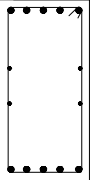TYPE	SLOOF S1 (300 x 600)		
	TUMP. KIRI	LAPANGAN	TUMP. KANAN
POTONGAN			
TUL. ATAS	5 D19	5 D19	5 D19
TUL. BAWAH	5 D19	5 D19	5 D19
SENGKANG	D 10 - 100	D 10 - 200	D 10 - 100
TUL. PINGGANG	2 D 10		

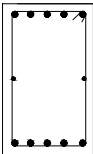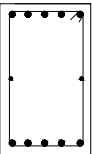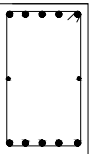TYPE	SLOOF S2 (300 x 500)		
	TUMP. KIRI	LAPANGAN	TUMP. KANAN
POTONGAN			
TUL. ATAS	5 D19	5 D19	5 D19
TUL. BAWAH	5 D19	5 D19	5 D19
SENGKANG	D 10 - 100	D 10 - 200	D 10 - 100
TUL. PINGGANG	2 D 10		


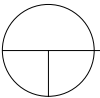


DETAIL STRUKTUR


SKALA 1:25 PAPER A3

KETERANGAN			
REVISI			
NO.	URAIAN	TANGGAL	PARAF
PEMBERI TUGAS :			
NAMA PROYEK :			
PERENCANAAN DED PRIMAHUSADA SUKOREJO			
MENGETAHUI:			
PEMILIK			
KONSULTAN PERENCANA :			
 PT.ASKA MULIA ANOPAMA <i>architecture.interior.and urban design</i> Jl.Prambanan-Piyungan KM.1,5 no.8 Ngoro-Oro, Ringinsari, Bokoharjo, Prambanan, Sleman, Yogyakarta, 55572			
PENANGGUNG JAWAB ARSITEKTUR:			
 AGUS SETIAWAN,ST.,M.Arch.,IAI,GP AHLI ARSITEK–MADYA			
PENANGGUNG JAWAB STRUKTUR:			
 WAHYU HENDRATNO, ST AHLI TEKNIK BANGUNAN GEDUNG–MADYA			
PENANGGUNG JAWAB MEKANIKAL–ELEKTRIKAL–PLUMBING:			
 NOVA NURDIANSYAH, ST AHLI TEKNIK TENAGA LISTRIK–MADYA			
NAMA GAMBAR :			
DETAIL STRUKTUR			
NO. PROYEK :		TANGGAL :	
–		DIGAMBAR :	
SATUAN UKURAN :		DIPERIKSA :	
		DISETUJUI :	
SKALA	NO. GAMBAR	NO. REVISI	NO. LEMBAR
1:25 PAPER A3	S.7.03		17



DETIL KOLOM K1 HB 400x400
SKALA 1 : 15

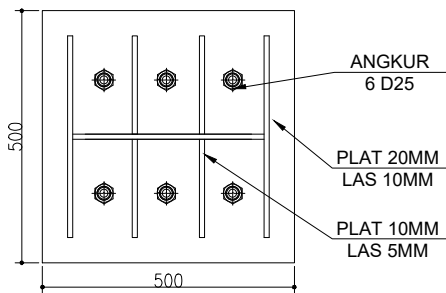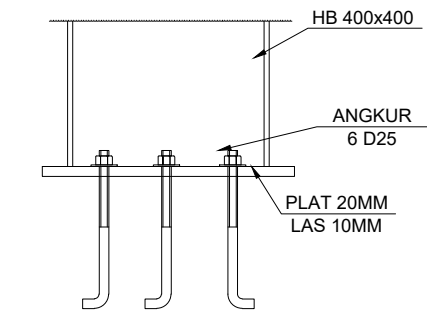


DETIL B1 KE KOLOM
SKALA 1 : 15

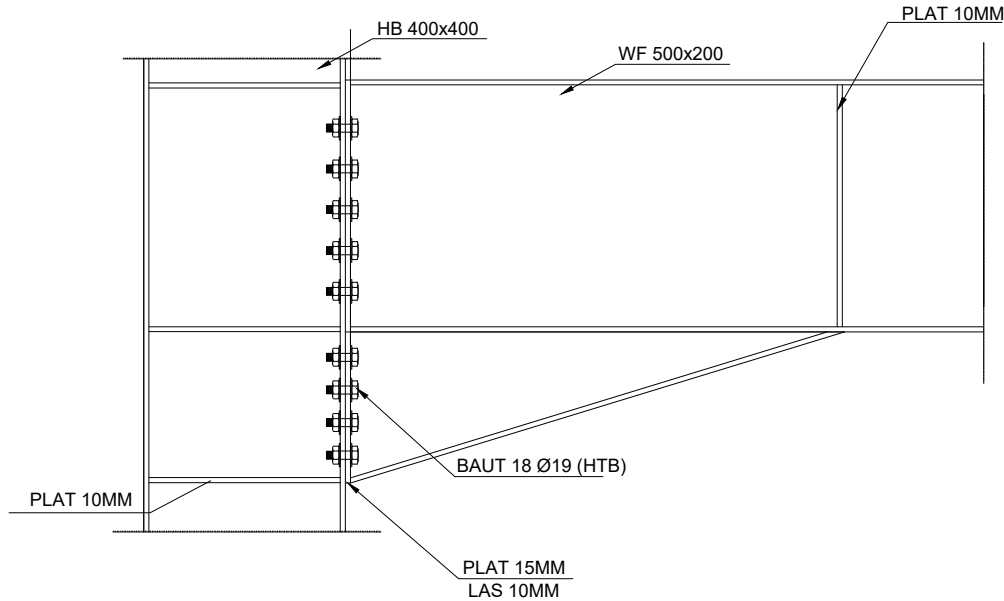


DETIL B3 KE KOLOM
SKALA 1 : 15







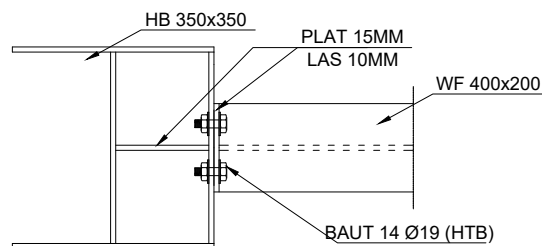
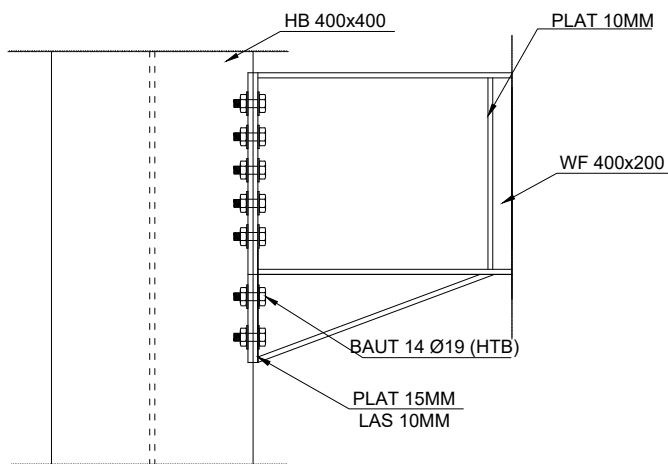



DETIL B2 KE KOLOM
SKALA 1 : 15

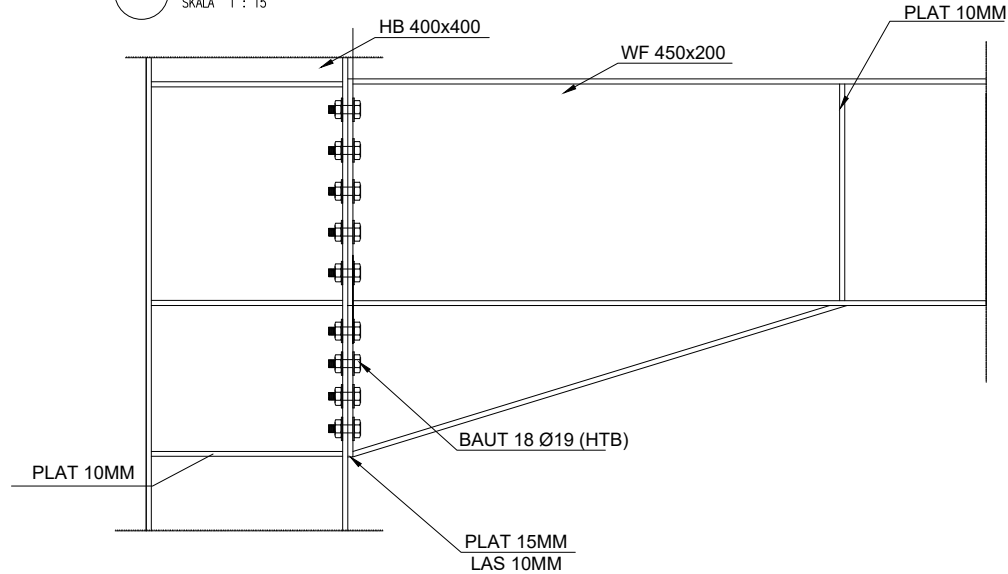

DETAIL STRUKTUR
SKALA 1:15 PAPER A3

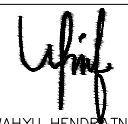KETERANGAN			
REVISI			
NO.	URAIAN	TANGGAL	PARAF
PEMBERI TUGAS :			
NAMA PROYEK :			
PERENCANAAN DED PRIMAUSADA SUKOREJO			
MENGETAHUI:			
PEMILIK			
KONSULTAN PERENCANA :			
 PT.ASKA MULIA ANOPAMA <i>architecture.interior.and urban design</i> Jl.Prambanan-Piyungan KM.1,5 no.8 Ngoro-Oro, Ringinsari, Bokoharjo, Prambanan, Sleman, Yogyakarta, 55572			
PENANGGUNG JAWAB ARSITEKTUR:			
 AGUS SETIAWAN,ST.,M.Arch.,IAI,GP AHLI ARSITEK-MADYA			
PENANGGUNG JAWAB STRUKTUR:			
 WAHYU HENDRATNO, ST AHLI TEKNIK BANGUNAN GEDUNG-MADYA			
PENANGGUNG JAWAB MEKANIKAL-ELEKTRIKAL-PLUMBING:			
 NOVA NURDIANSYAH, ST AHLI TEKNIK TENAGA LISTRIK-MADYA			
NAMA GAMBAR :			
DETAIL STRUKTUR			
NO. PROYEK :		TANGGAL :	
-		DIGAMBAR :	
SATUAN UKURAN :		DIPERIKSA :	
		DISETUJUI :	
SKALA	NO. GAMBAR	NO. REVISI	NO. LEMBAR
1:15 PAPER A3	S.7.04		18

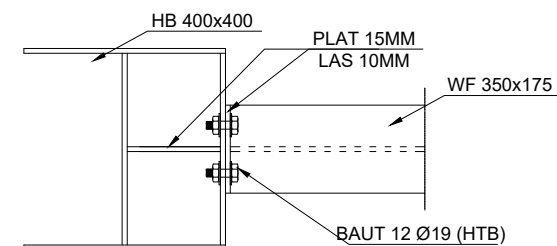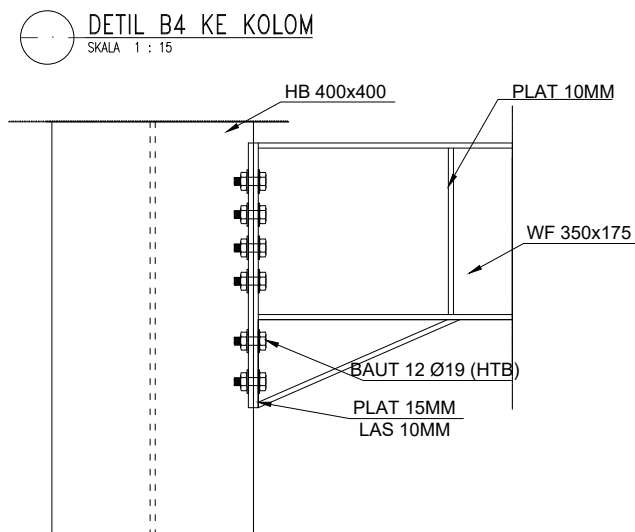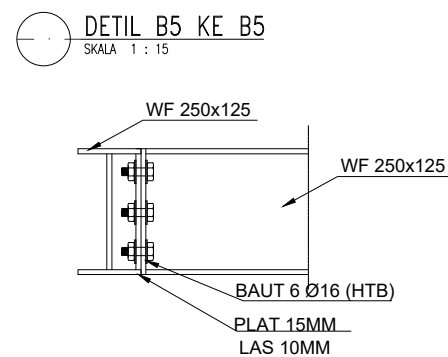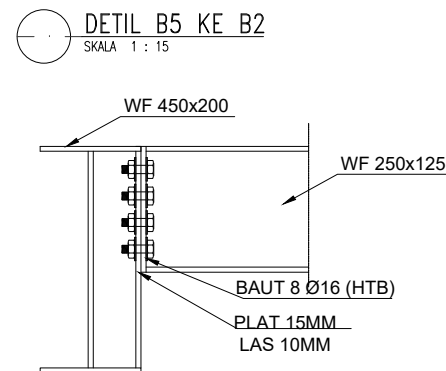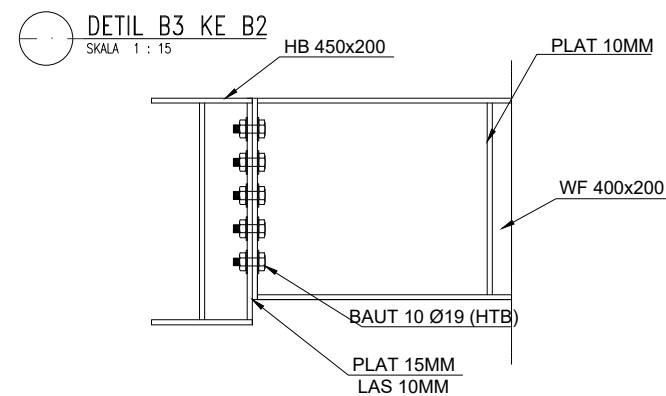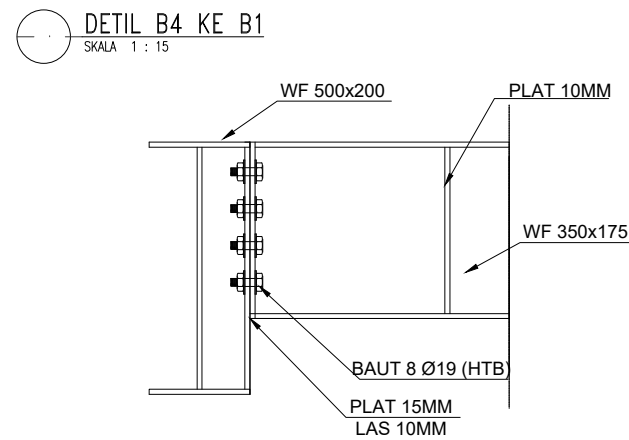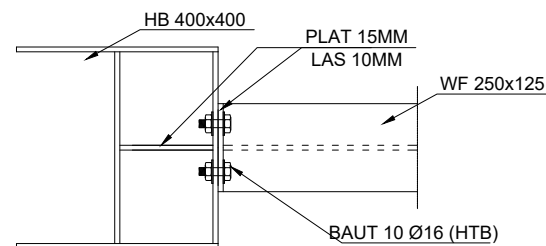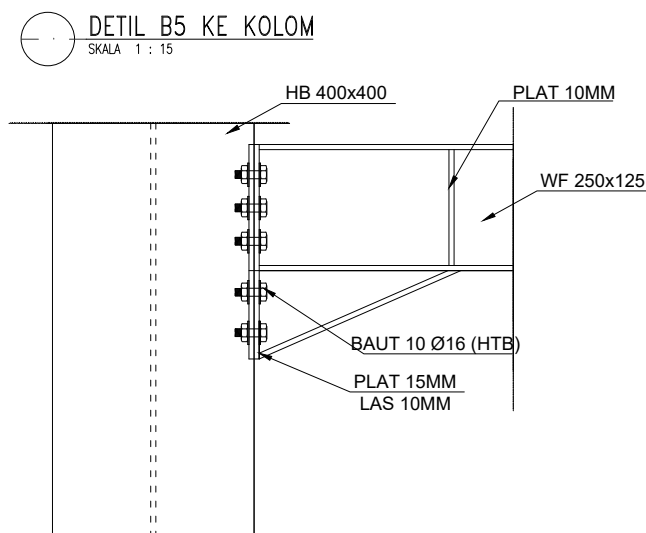

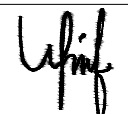KETERANGAN			
REVISI			
NO.	URAIAN	TANGGAL	PARAF
PEMBERI TUGAS :			
NAMA PROYEK :			
PERENCANAAN DED PRIMAUSADA SUKOREJO			
MENGETAHUI:			
PEMILIK			
KONSULTAN PERENCANA :			
 PT. ASKA MULIA ANOPAMA <i>architecture, interior and urban design</i> Jl. Prambanan-Piyungan KM. 1,5 no.8 Ngoro-Oro, Ringinsari, Bokoharjo, Prambanan, Sleman, Yogyakarta, 55572			
PENANGGUNG JAWAB ARSITEKTUR:			
 AGUS SETIAWAN, ST., M. Arch., IAI, GP AHLI ARSITEK – MADYA			
PENANGGUNG JAWAB STRUKTUR:			
 WAHYU HENDRATNO, ST AHLI TEKNIK BANGUNAN GEDUNG – MADYA			
PENANGGUNG JAWAB MEKANIKAL – ELEKTRIKAL – PLUMBING:			
 NOVA NURDIANSYAH, ST AHLI TEKNIK TENAGA LISTRIK – MADYA			
NAMA GAMBAR :			
DETAIL STRUKTUR			
NO. PROYEK :		TANGGAL :	
-		DIGAMBAR :	
SATUAN UKURAN :		DIPERIKSA :	
		DISETUJUI :	
SKALA	NO. GAMBAR	NO. REVISI	NO. LEMBAR
1:15 PAPER A3	S.7.05		19